

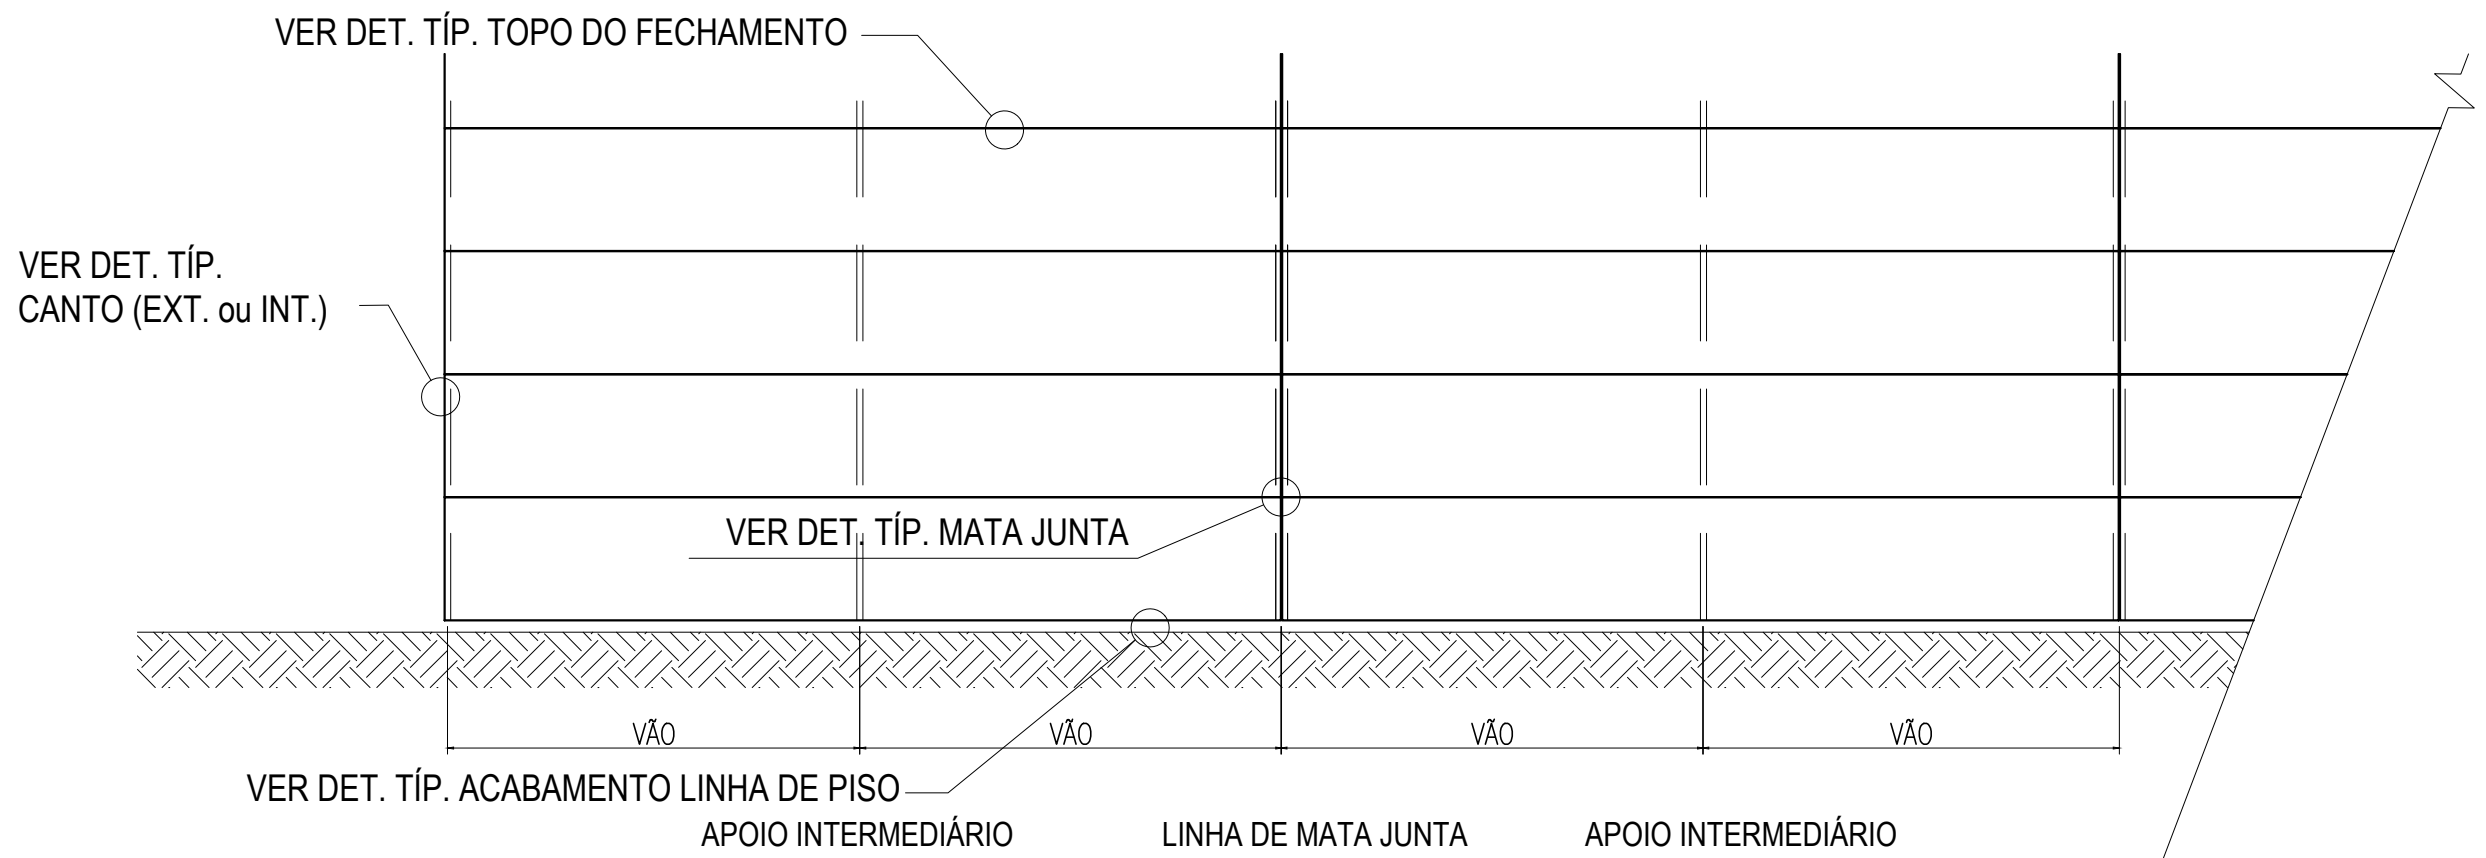


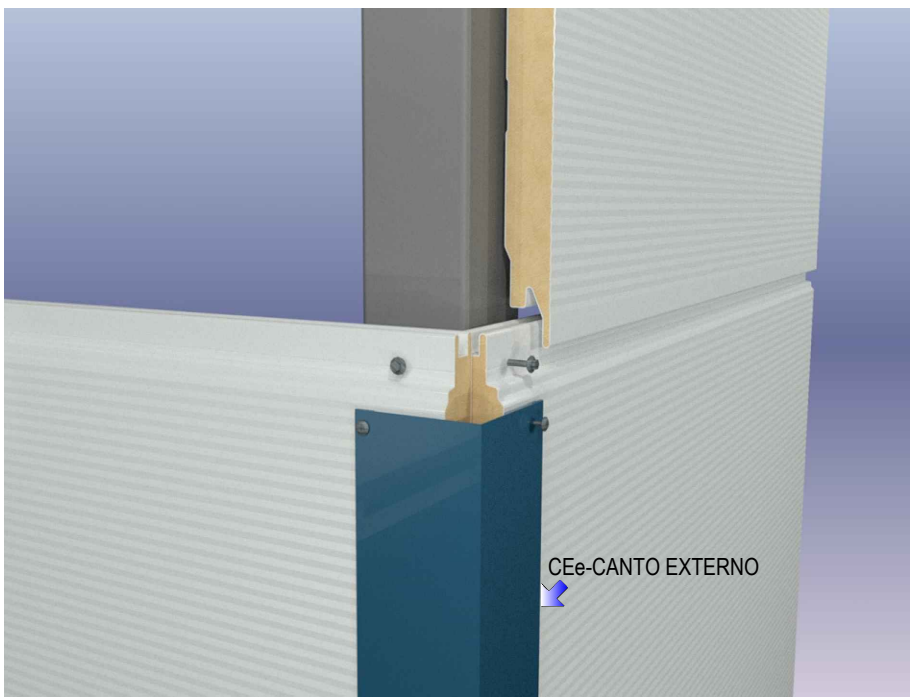


ELEVAÇÃO FECH. HORIZONTAL PAINEL TW50-MN

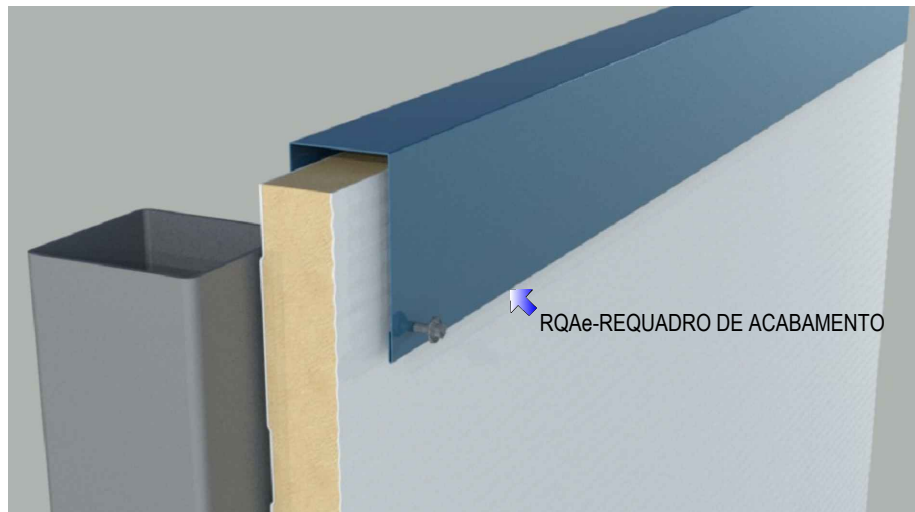


DET. TÍP. TOPO DO FECHAMENTO

IMPORTANTE
A DEFINIÇÃO DOS ACABAMENTO SUPERIORES
PODE MUDAR EM FUNÇÃO DAS NECESSIDADES DO
DO PROJETO.


IMPORTANTE
PREVER APOIOS RESPEITANDO OS LIMITES DE VÃO
PARA O PAINEL TW50MN CONFORME GUIA DE
ESPECIFICAÇÃO DO PRODUTO.

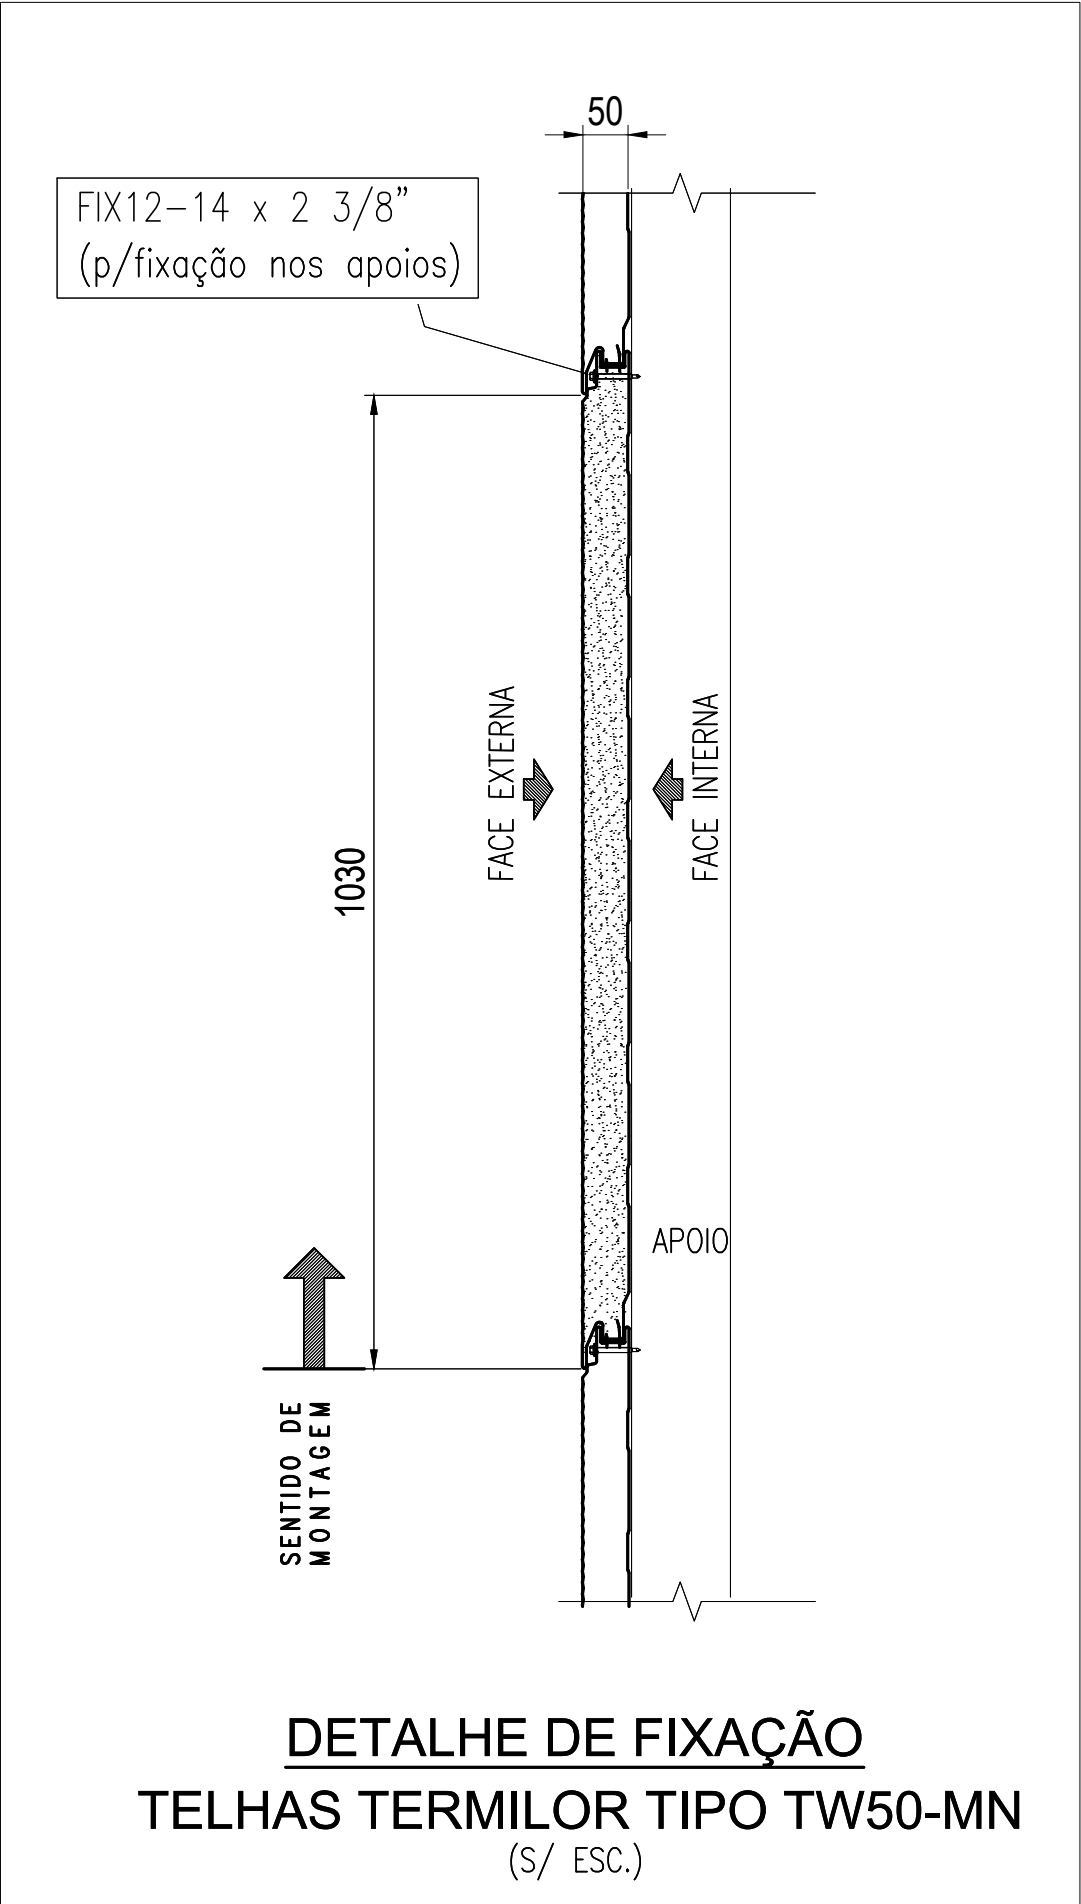



DETALHE DE FIXAÇÃO
TELHAS TERMILOR TIPO TW50-MN
(S/ ESC.)

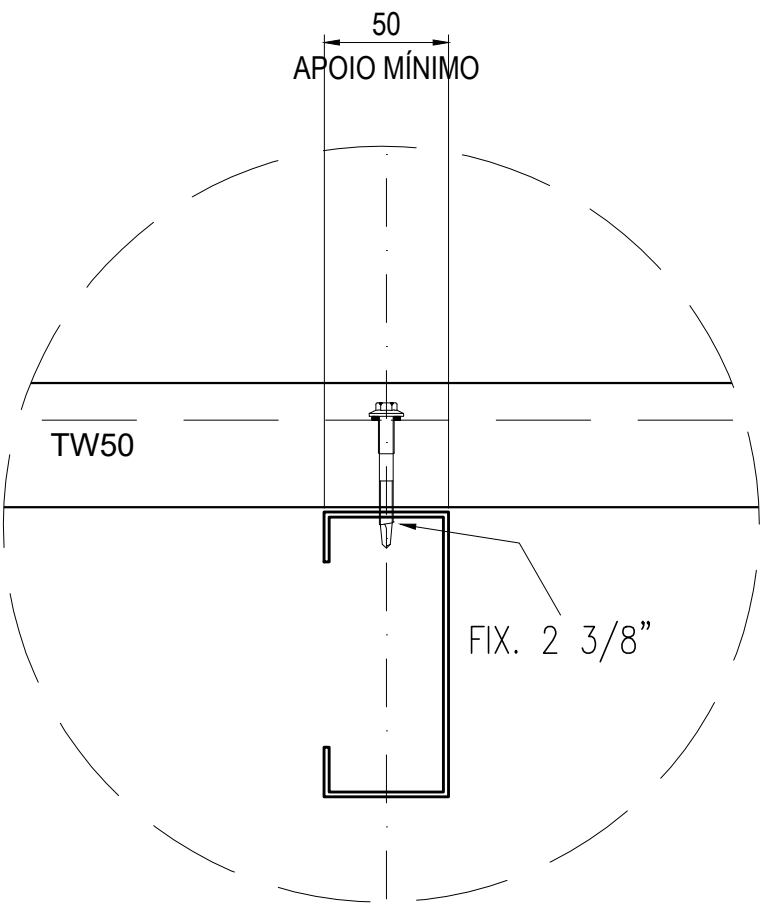


DETALHE APOIO MÍNIMO
PARA FIXAÇÃO DE UM PAINEL
ESC.1:7,5

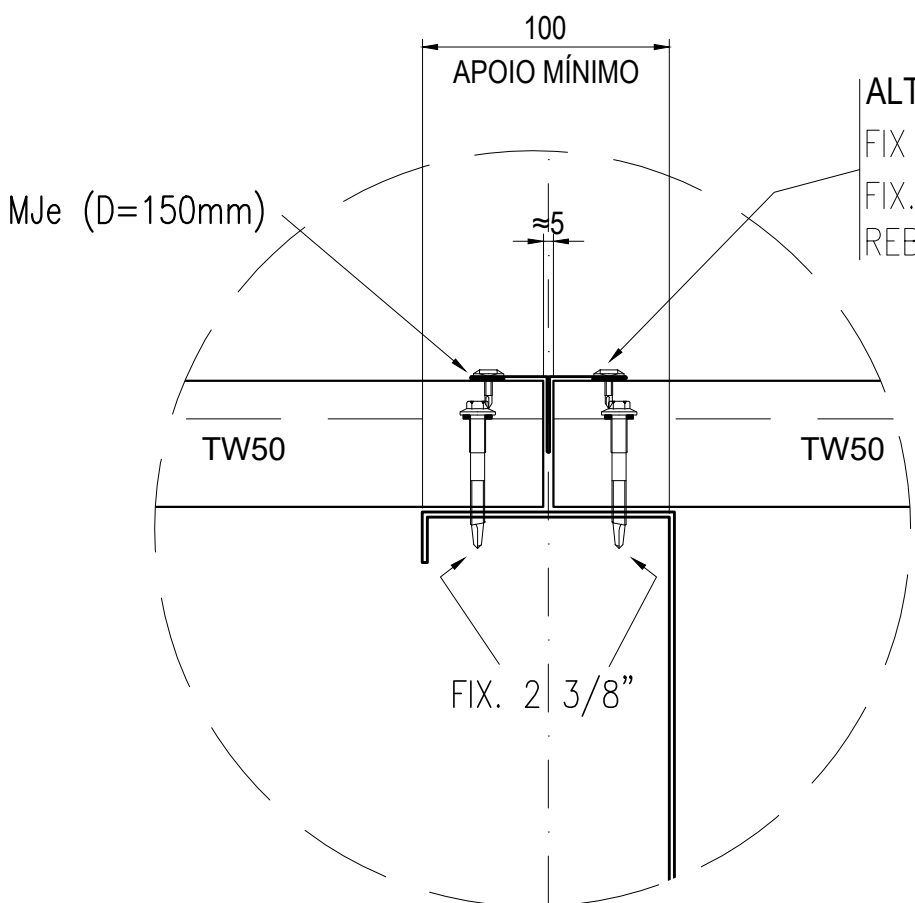

DETALHE APOIO MÍNIMO
PARA FIXAÇÃO DE DOIS PAINELIS
(CHEGADA DE TOPO)
ESC.1:7,5

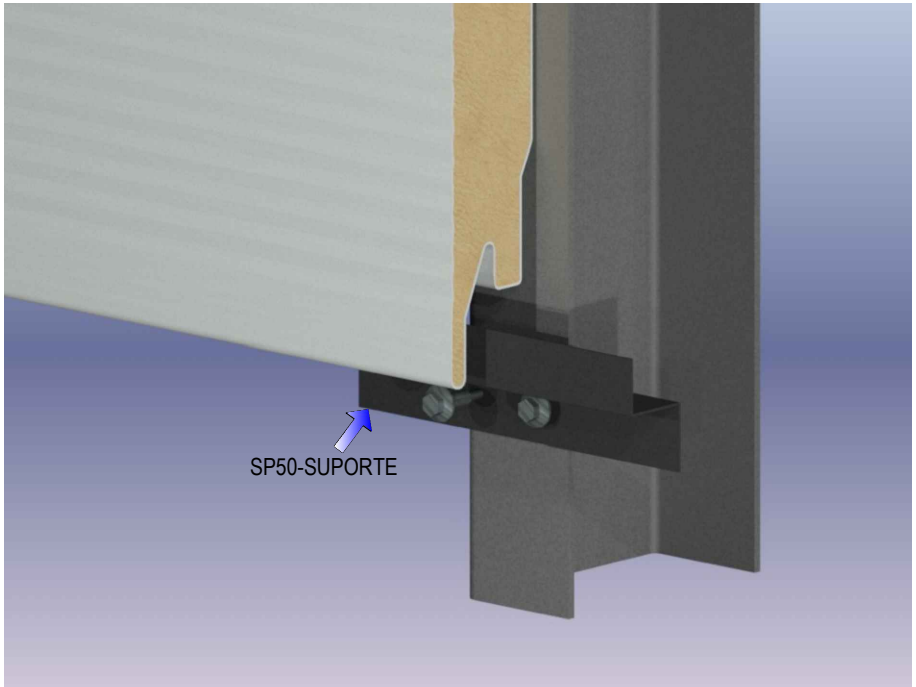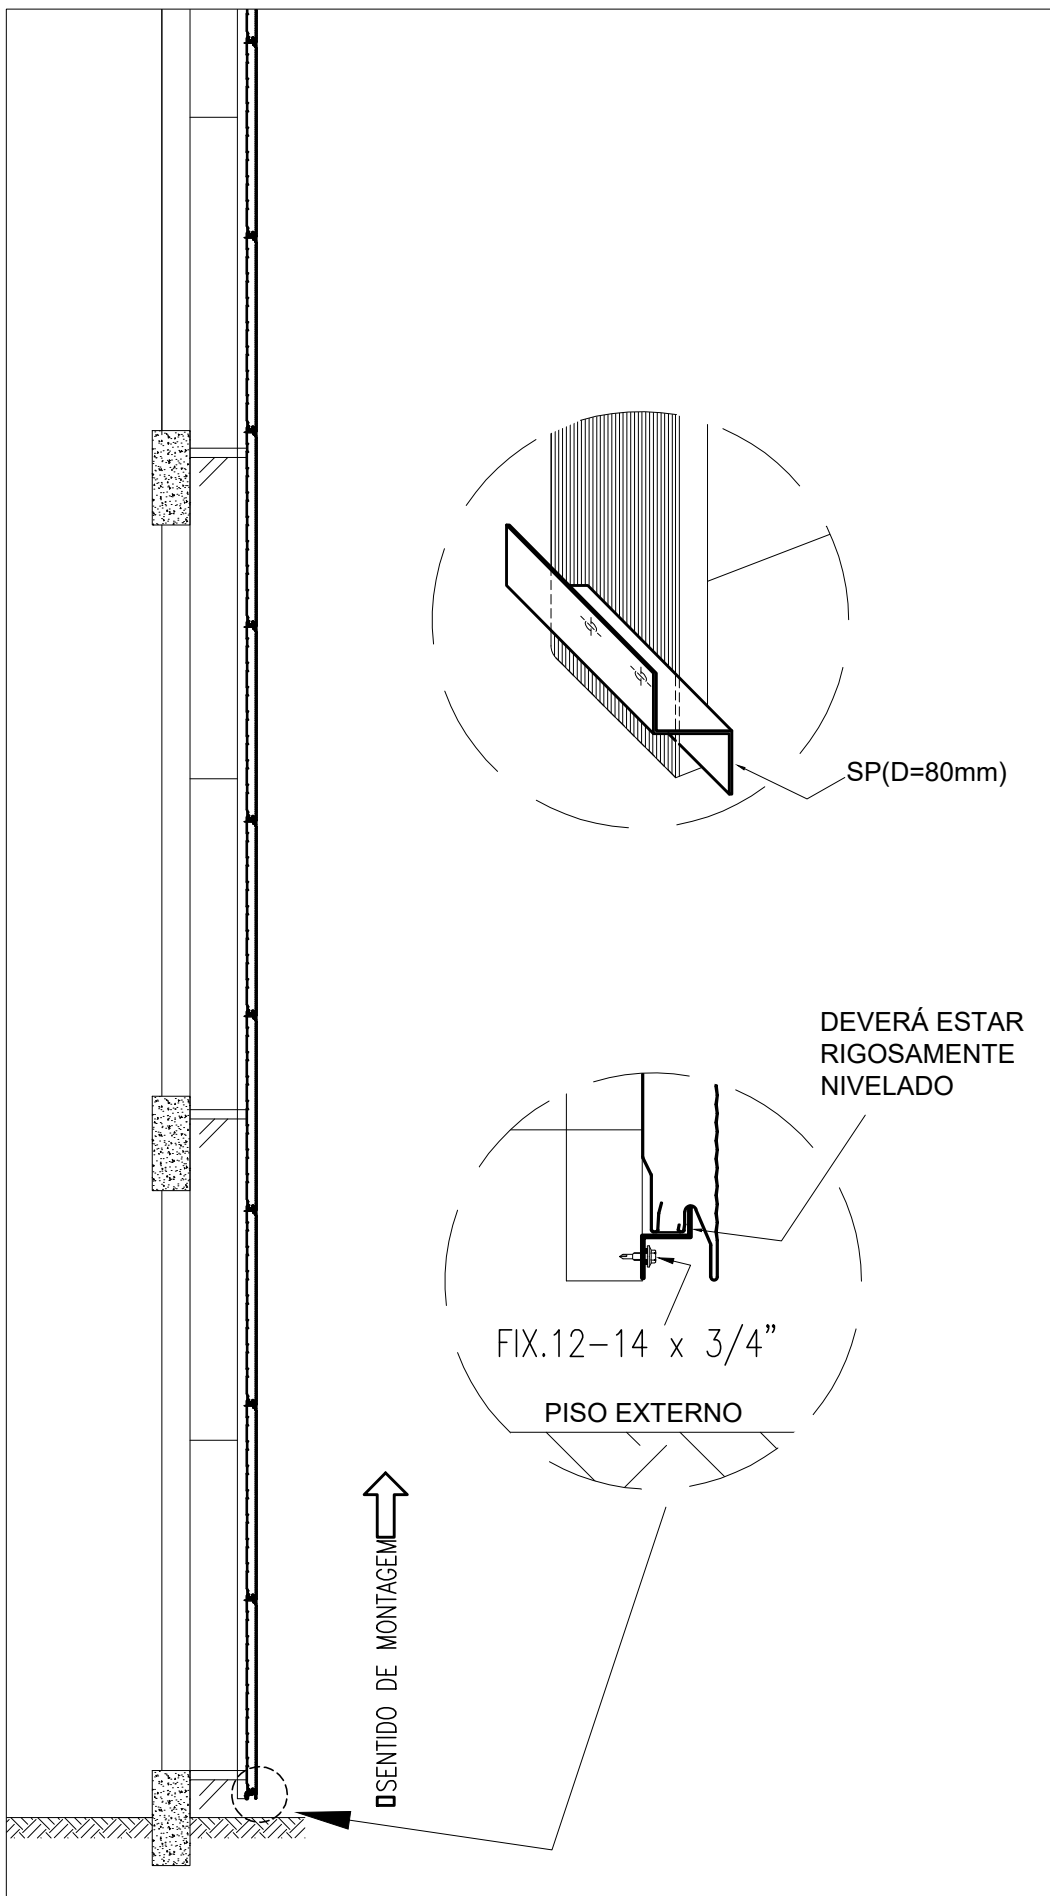

DET. TÍPICO SUPORTE SAÍDA DE MONTAGEM

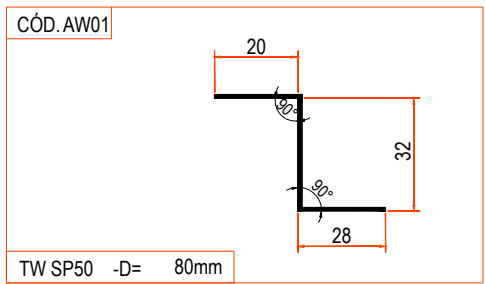

DET. TÍPICO ENCONTRO DE TOPO - MJe-MATA JUNTA

NOTAS GERAIS:

- 1 - DIMENSÕES EM MILÍMETROS.
- 2 - N.F.P. = NÃO FORNECIDO PELA PERFILOR.
- 3 - TODOS OS RECORTES NECESSÁRIOS DEVERÃO SER EXECUTADOS NA OBRA.
- 4 - ACABAMENTO COBERTURA E FECHAMENTO: VER LISTA DE MATERIAL
- 5 - SISTEMA DE PAINEL NERVURADO COM ISOLAMETO TÉRMICO E ACÚSTICO EM ESPUMA DE POLIISOCIANURATO (PIR) 50mm DENSIDADE: 38KG/m3
- 6 - OS PAINELIS TW50 NÃO SÃO PRODUZIDOS COM COMPRIMENTO INFERIOR A 3000mm
- 7 - O CLIENTE DEVERÁ CONFIRMAR GEOMETRIA E MEDIDAS DOS ARREMATES INDICADOS OU ADQUIRIR CHAPAS (1,2X3,0m) PARA FABRICAÇÃO NA OBRA.

- DESENHOS DE REFERENCIA :

0	EMISSÃO INICIAL	06/10/2021	AMCF			
REVISÃO	DESCRIÇÃO	DATA	EXEC.	VERIF.	APROV.	
DATA: 06/10/2021	FINALIDADE: ILUSTRATIVO	DESENHADO POR: AMCF	REVISADO POR: DAO	APROVADO POR:	PRODUTO: TW50-MN	



www.perflor.com.br

Tel.(11) 3065-3400

projetos@perflor.com.br

CLIENTE / PROPRIETARIO

TÍTULO
DETALHES ILUSTRATIVOS
FECHAMENTO TW50-MN HORIZONTAL

LOCAL DA OBRA	REFS.	OBRA N.º	DESENHO N.º	FOLHA N.º	REV.
	SP20	0000	0000	22 ÚNICA	0

• FICA PROIBIDA A REPRODUÇÃO TOTAL OU PARCIAL DESTES DESENHOS SEM AUTORIZAÇÃO POR ESCRITO DA PERFILOR