

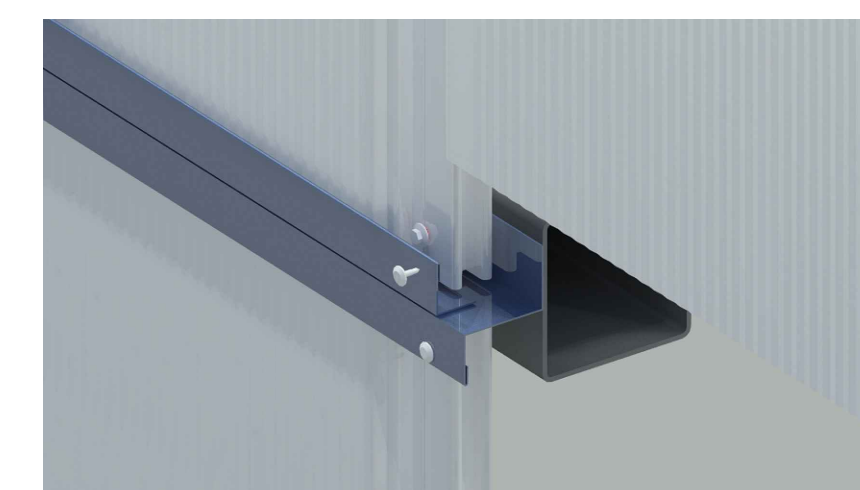
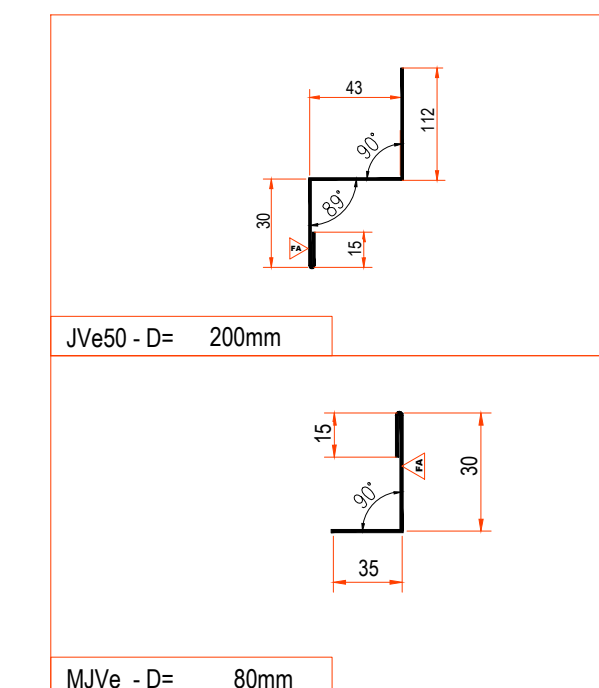
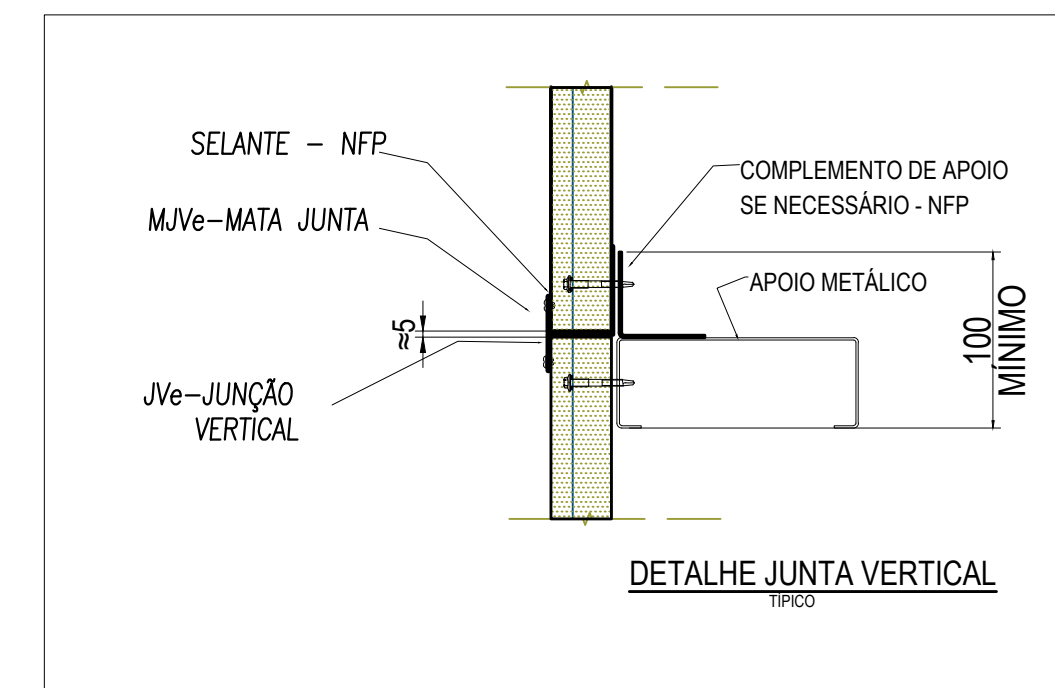
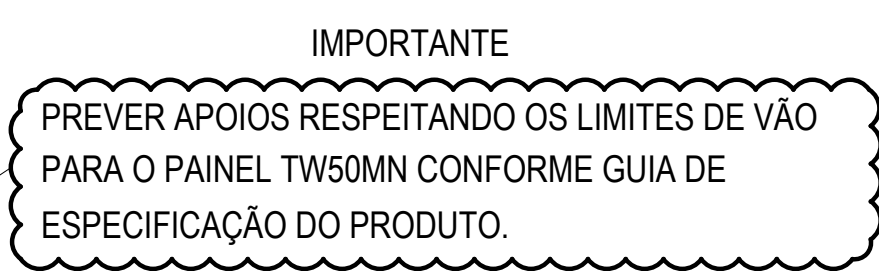
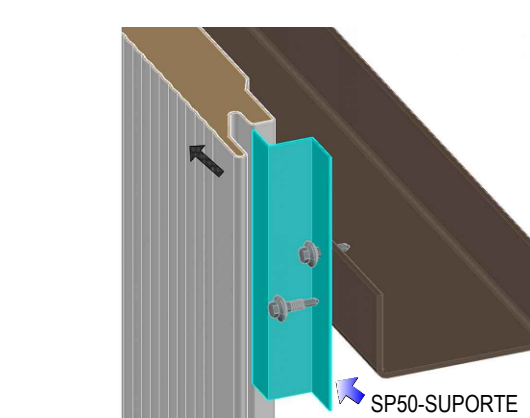
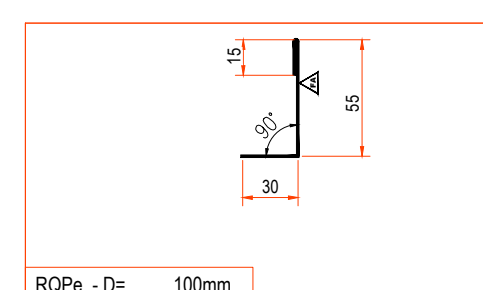
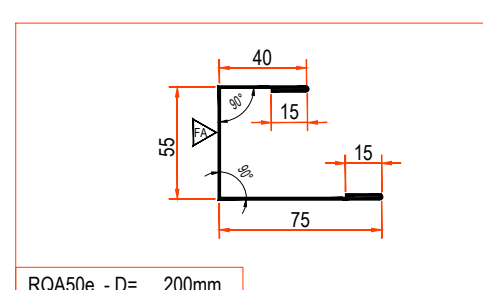
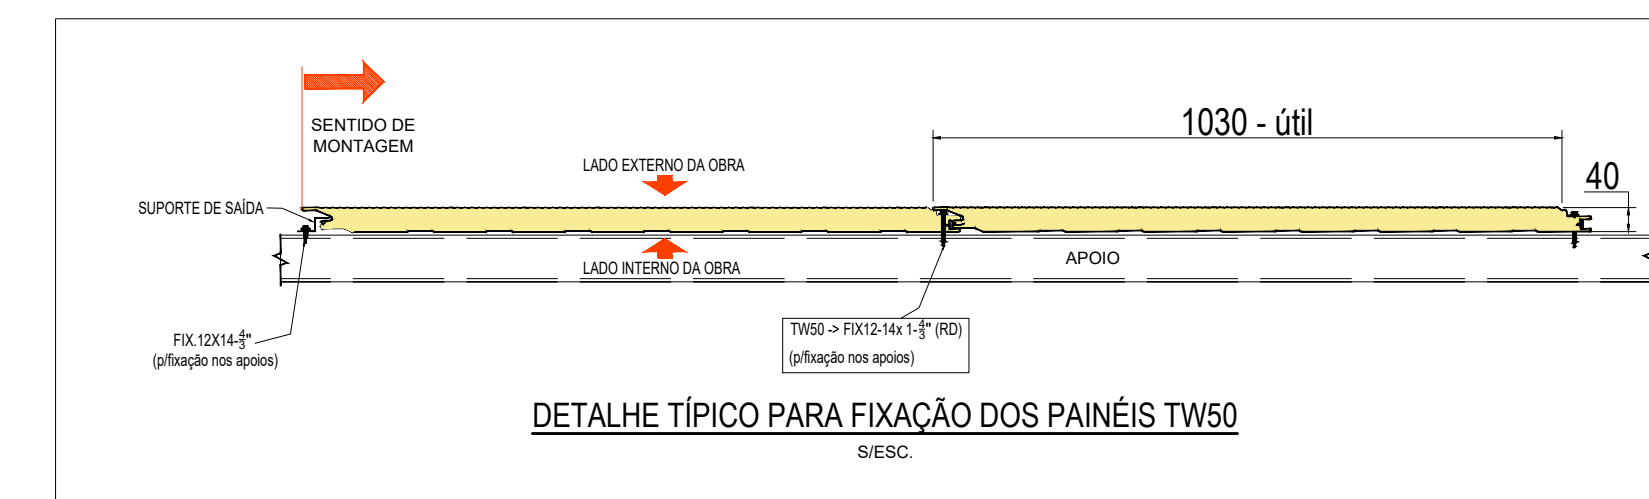
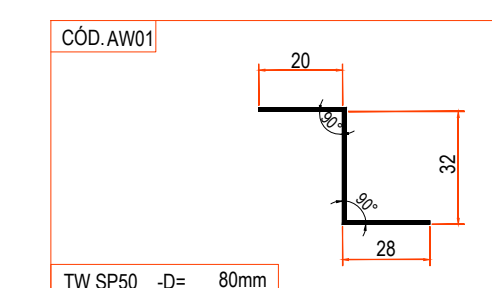
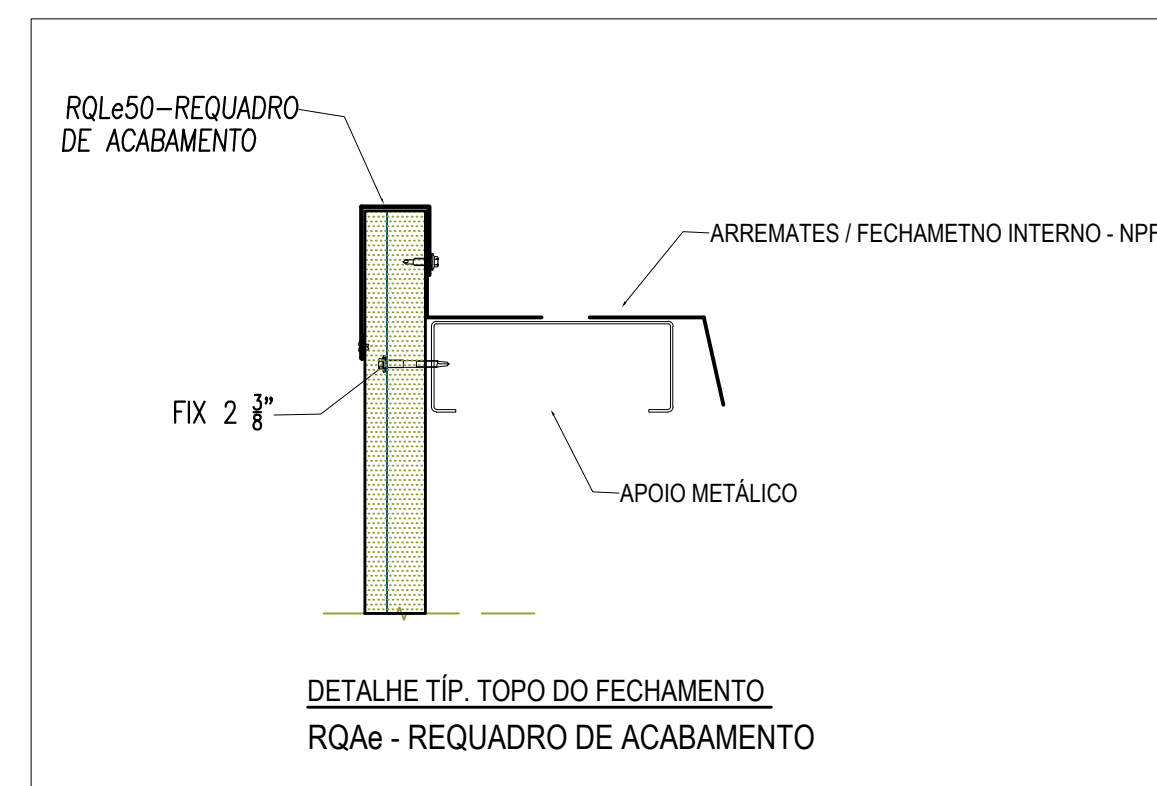


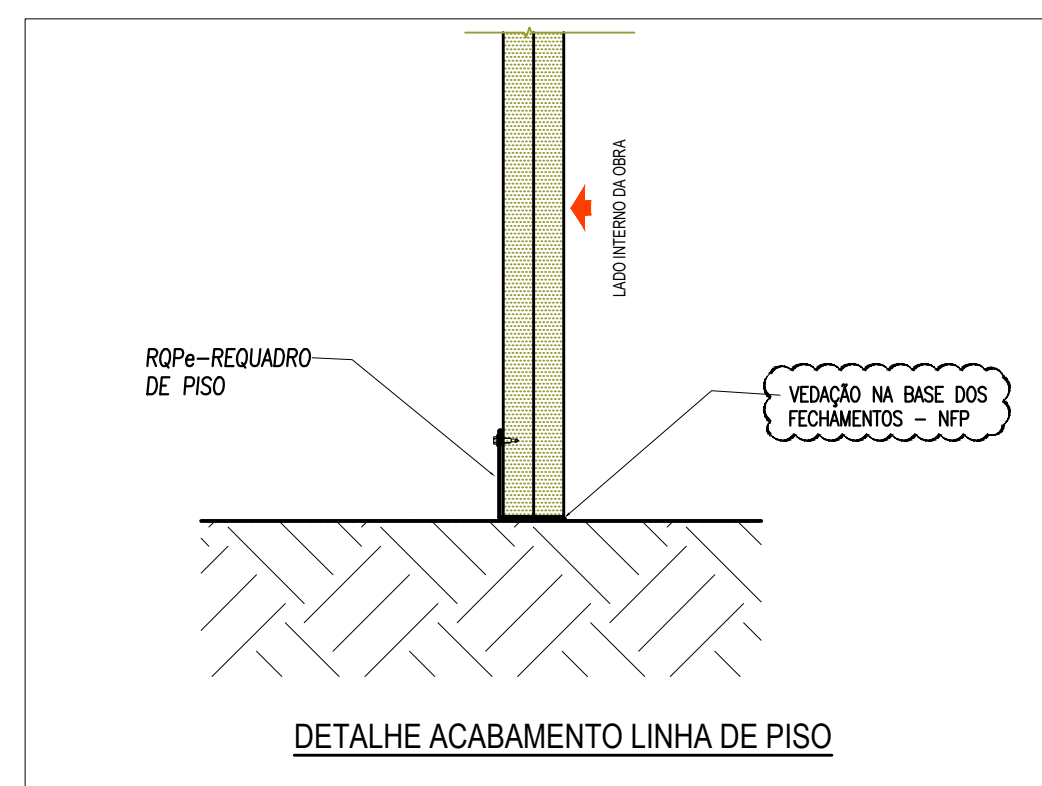

IMPORTANTE
 A DEFINIÇÃO DOS ACABAMENTO SUPERIORES
 PODE MUDAR EM FUNÇÃO DAS NECESSIDADES
 DO PROJETO.

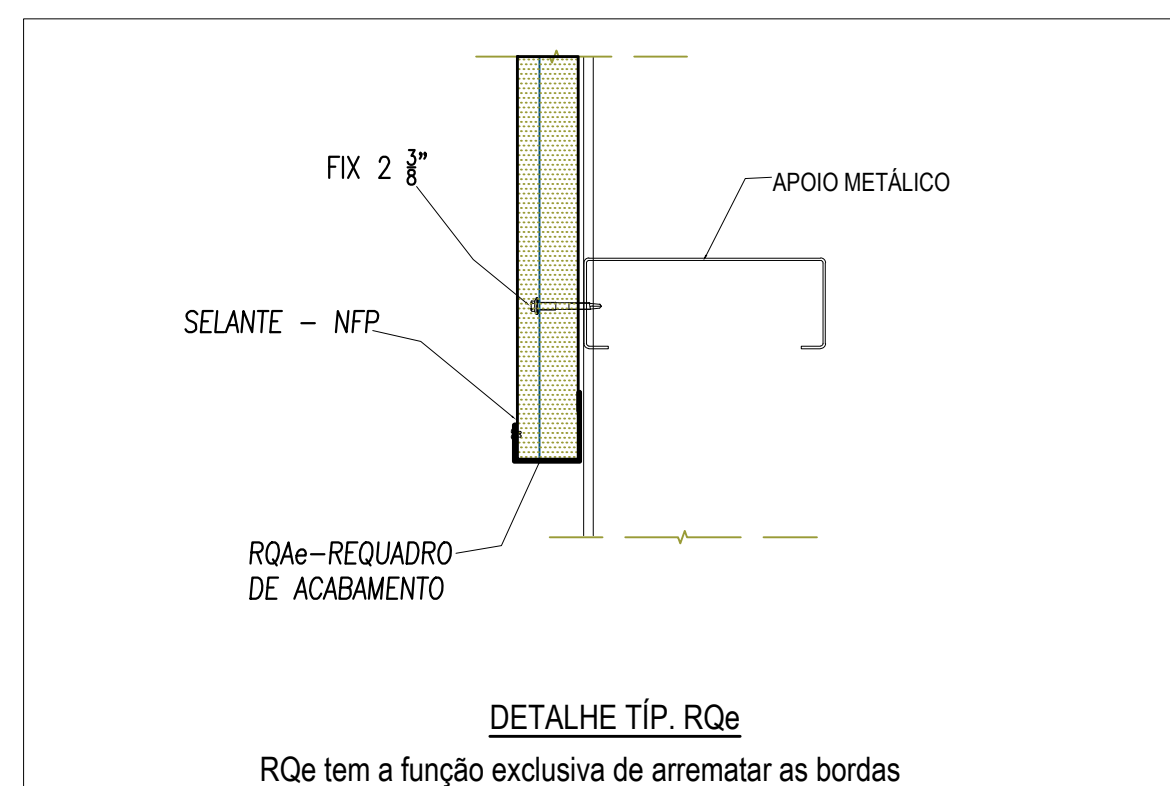


DET. TÍPICO SUPORTE SAÍDA DE MONTAGEM





NOTAS GERAIS:

- 1 - DIMENSÕES EM MILÍMETROS.
- 2 - N.F.P. = NÃO FORNECIDO PELA PERFILOR.
- 3 - TODOS OS RECORTES NECESSÁRIOS DEVERÃO SER EXECUTADOS NA OBRA.
- 4 - ACABAMENTO COBERTURA E FECHAMENTO: VER LISTA DE MATERIAL
- 5 - SISTEMA DE PAINEL NERVURADO COM ISOLAMENTO TÉRMICO E ACÚSTICO EM ESPUMA DE POLISOCIANURATO (PIR) 50mm DENSIDADE 38KG/m3
- 6 - OS PAINÉIS TW50 NÃO SÃO PRODUZIDOS COM COMPRIMENTO INFERIOR A 3000mm
- 7 - O CLIENTE DEVERÁ CONFIRMAR GEOMETRIA E MEDIDAS DOS ARREMATES INDICADOS OU ADQUIRIR CHAPAS (1.2X3.0M) PARA FABRICAÇÃO NA OBRA.

- DESENHOS DE REFERENCIA :

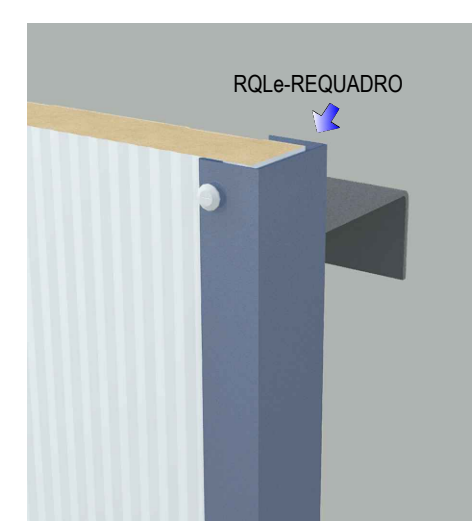


REQUADRO LATERAL DE ACABAMENTO

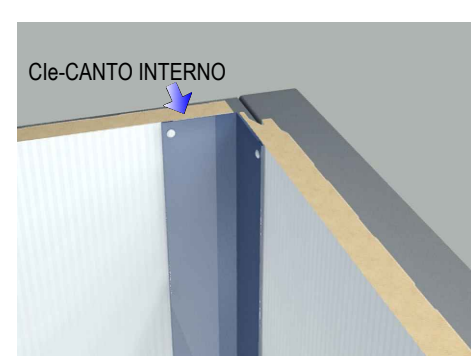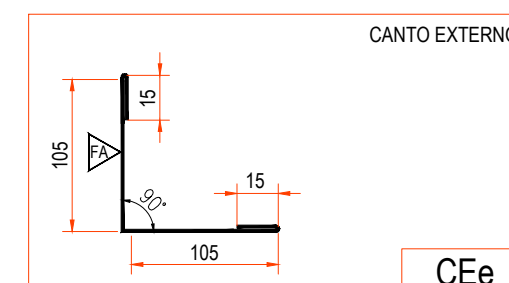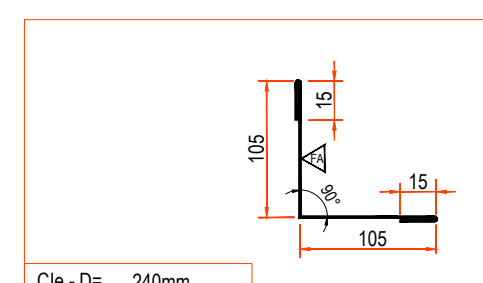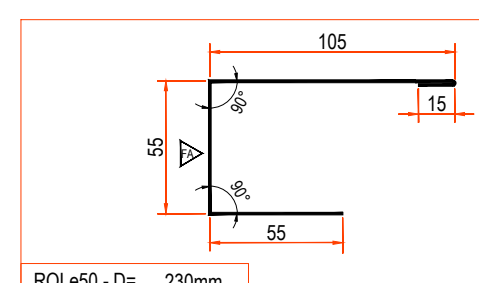

CANTO INTERNO



CANTO EXTERNO

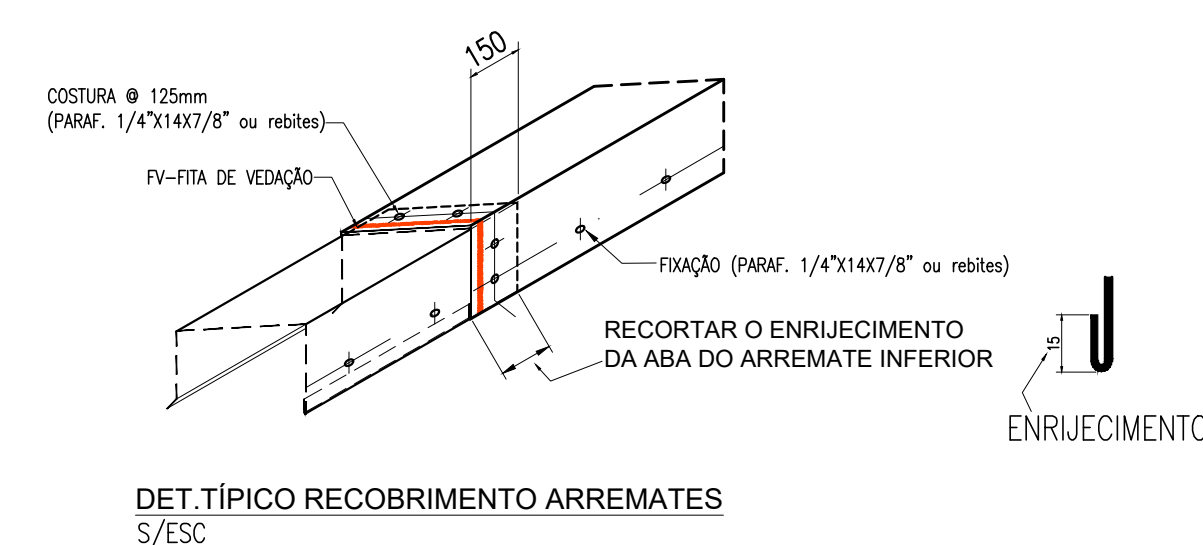DET.TÍPICO RECOBRIMIENTO ARREMATES
S/ESC

0	EMISSION INICIAL			06/10/2021	AMCF			
REVISAO	DESCRIÇÃO			DATA	EXEC.	VERIF.	APR.	
DATA: 06/10/2021	FINALIDADE: ILUSTRATIVO	DESENHADO POR: AMCF	REVISADO POR: DAO	APROVADO POR:	PRODUTO:	TIW50-MN		



www.perfilor.com.br

Tel.(11) 3065-3400

projetos@perfilor.com.br

CLIENTE / PROPRIETARIO

TITULO

DETALHES ILUSTRATIVOS

FECHAMENTO TW50-MN VERTICAL

LOCAL DA OBRA	REPRES.	OBRA N.º	DESENHO N.º	FOLHA N.º	REV.
	SP20	0000	0000 22	ÚNICA	0