


VILA GALE COLLECTION - BRUMADINHO

Country Resort Hotel das Artes, Conference & SPA

CADERNO DE PRANCHAS - MODELO BIM v91 (alta fidelidade)

- 01 BP - Planta de Eixos e Pilares
- 02 BP - Fachada Sul
- 03 BP - Fachada Leste
- 04 BP - Corte Longitudinal
- 05 BP - Corte Transversal
- 06 Bloco A - Planta Tipo
- 07 Bloco A - Fachada Sul
- 08 Bloco A - Corte Transversal
- 09 Bloco B - Planta Tipo
- 10 Bloco B - Fachada Sul
- 11 Cronograma 4D

BP - PLANTA DE EIXOS E PILARES

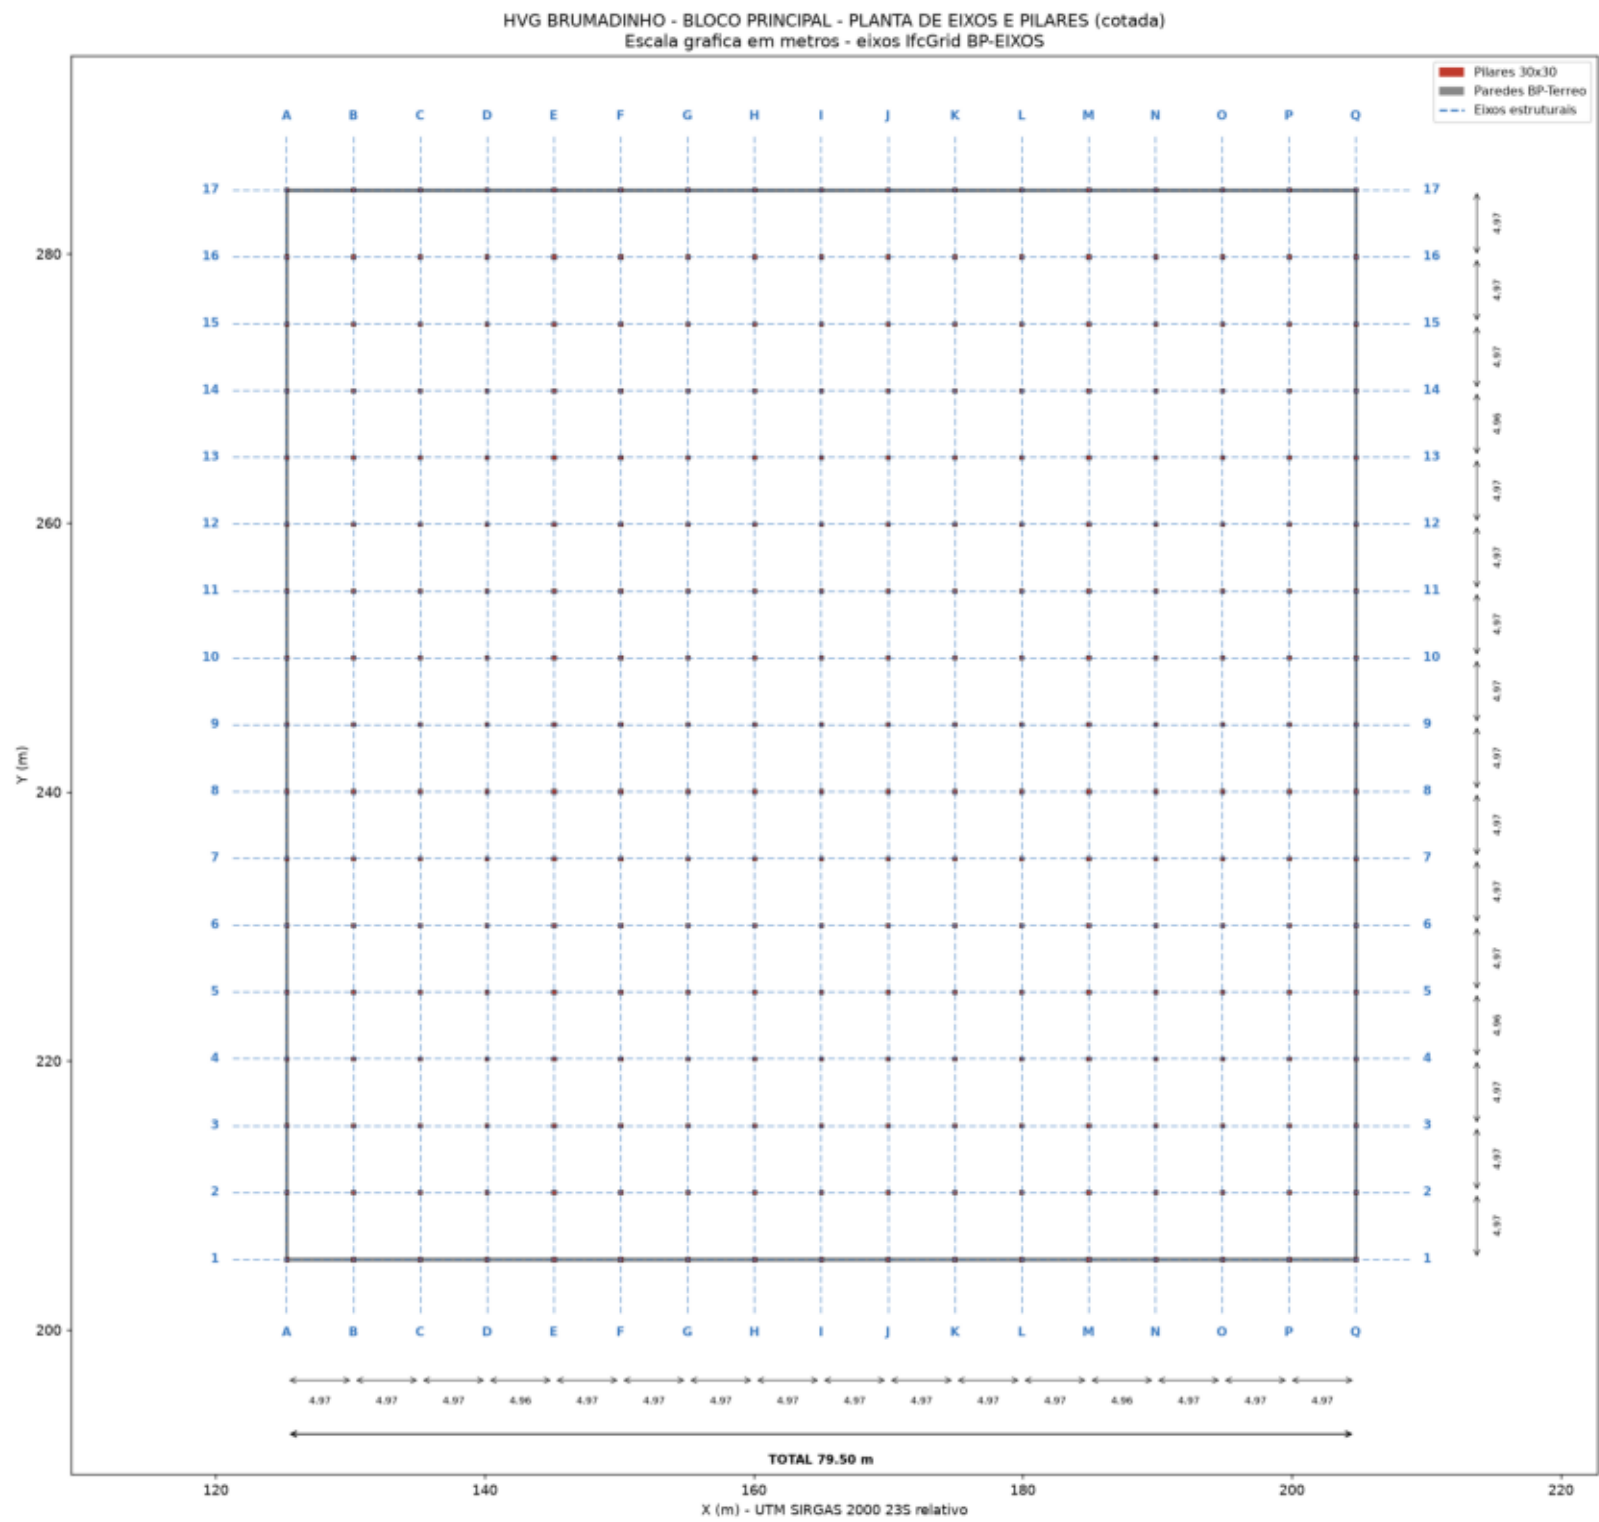

VILA GALE COLLECTION - BRUMADINHO


Country Resort Hotel das Artes, Conference & SPA

Planta de Eixos e Pilares - Bloco Principal

Grupo Montex Ltda - CREA 2101818418
Fase: Licenciamento Data: 06/2026

ESC: barra grafica

PRANCHA

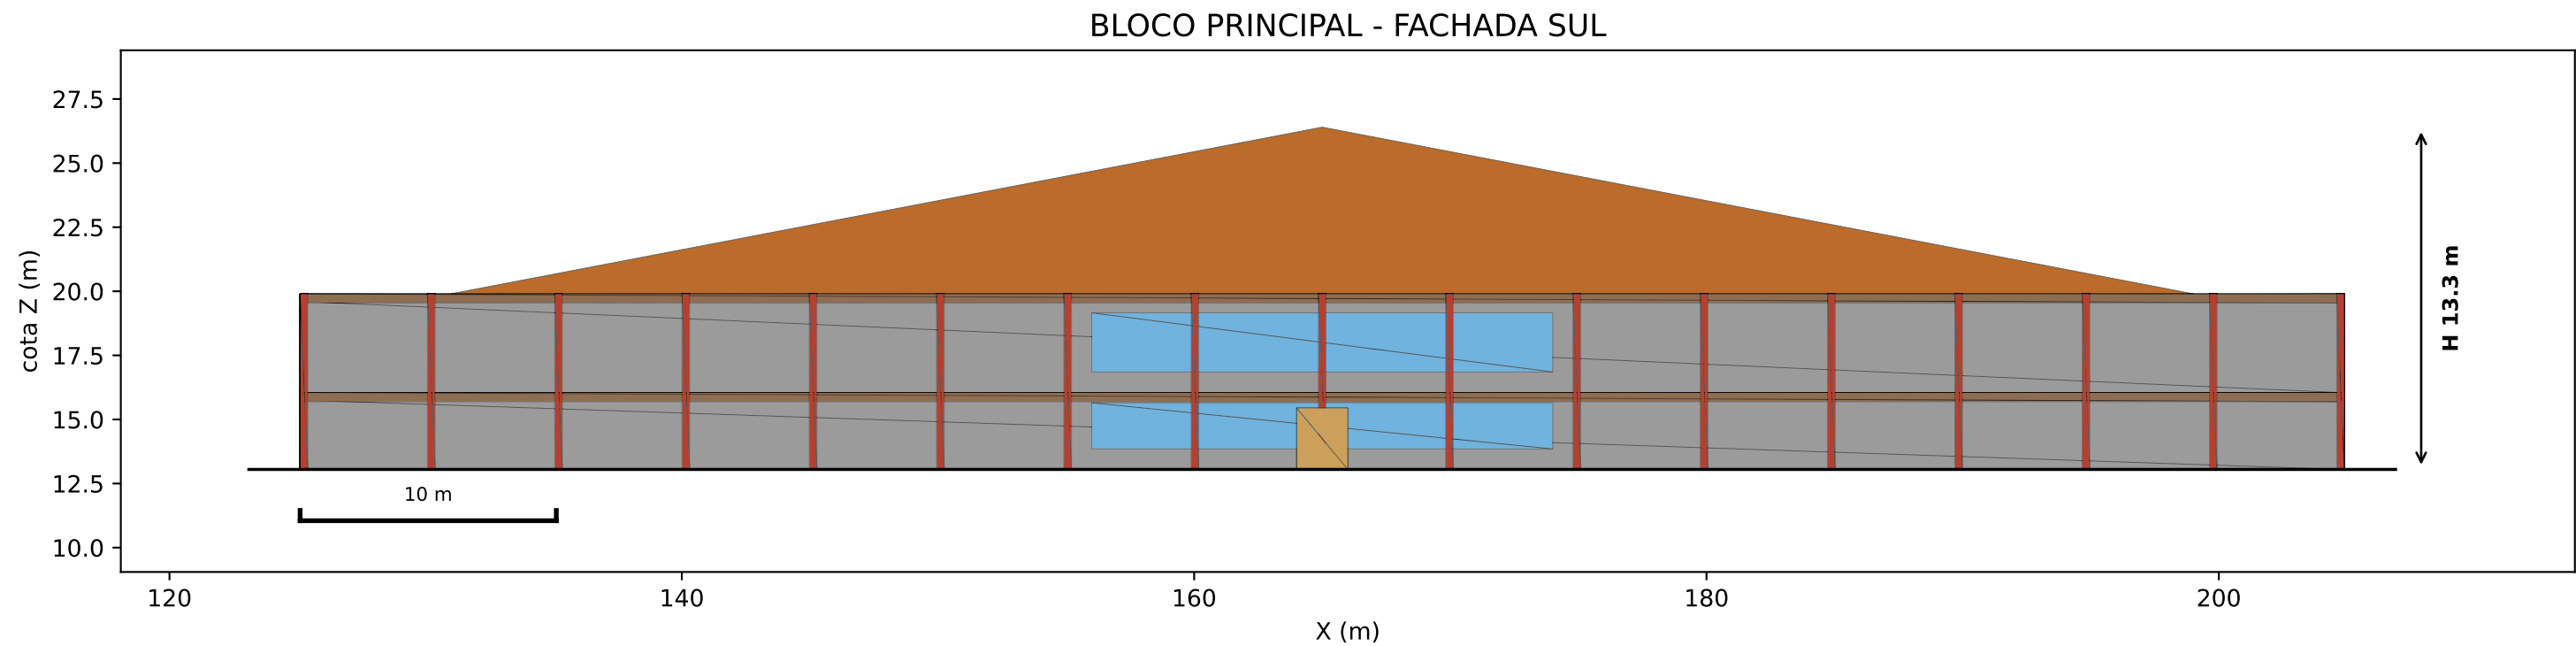

VILA GALE COLLECTION - BRUMADINHO

Country Resort Hotel das Artes, Conference & SPA


PRANCHA

Fachada Sul - Bloco Principal

Grupo Montex Ltda - CREA 2101818418
Fase: Licenciamento Data: 06/2026

ESC: barra grafica

02

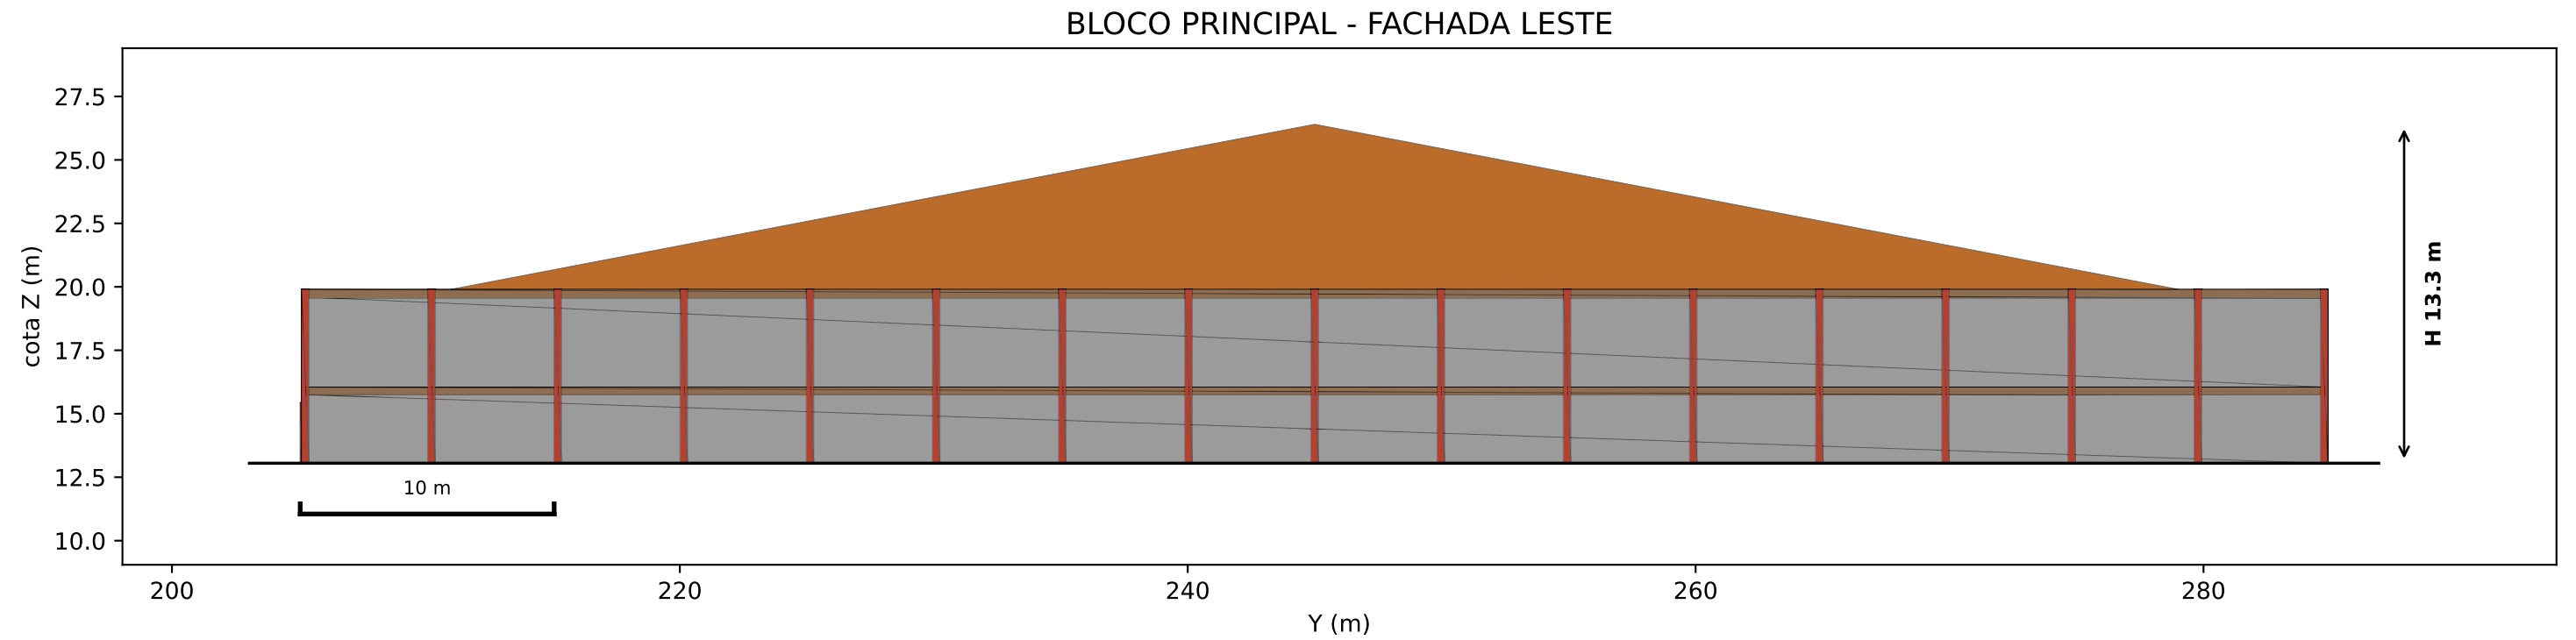

VILA GALE COLLECTION - BRUMADINHO

PRANCHA

Country Resort Hotel das Artes, Conference & SPA


Fachada Leste - Bloco Principal


03

Grupo Montex Ltda - CREA 2101818418
Fase: Licenciamento Data: 06/2026

ESC: barra grafica


BLOCO PRINCIPAL - CORTE LONGITUDINAL (Y=245)

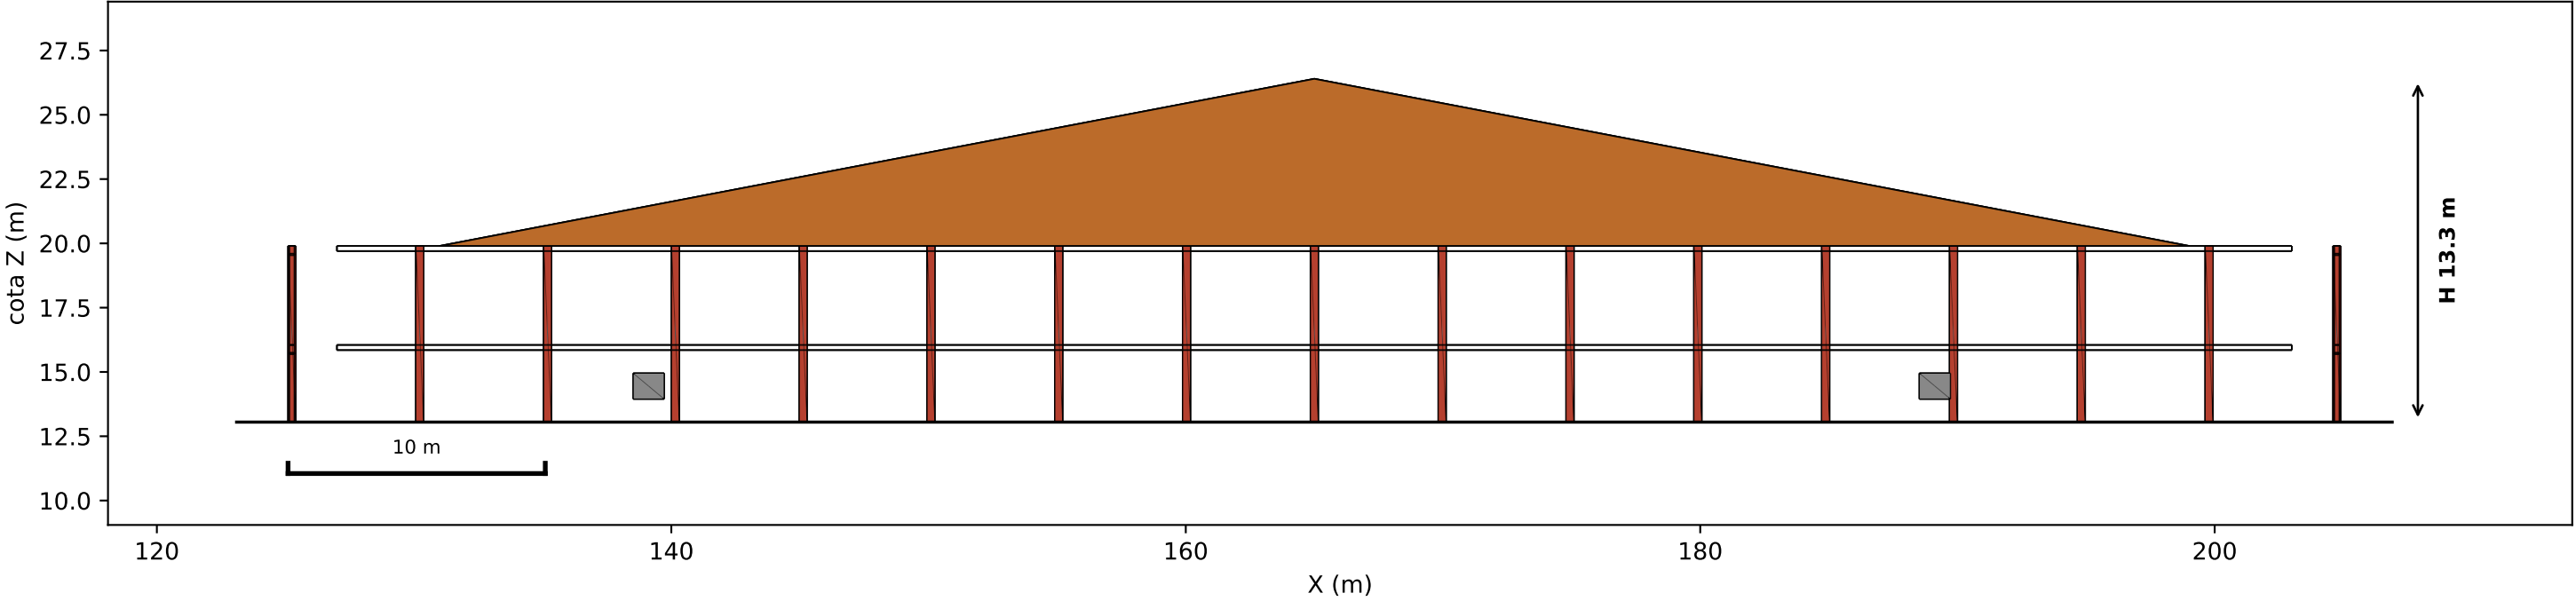

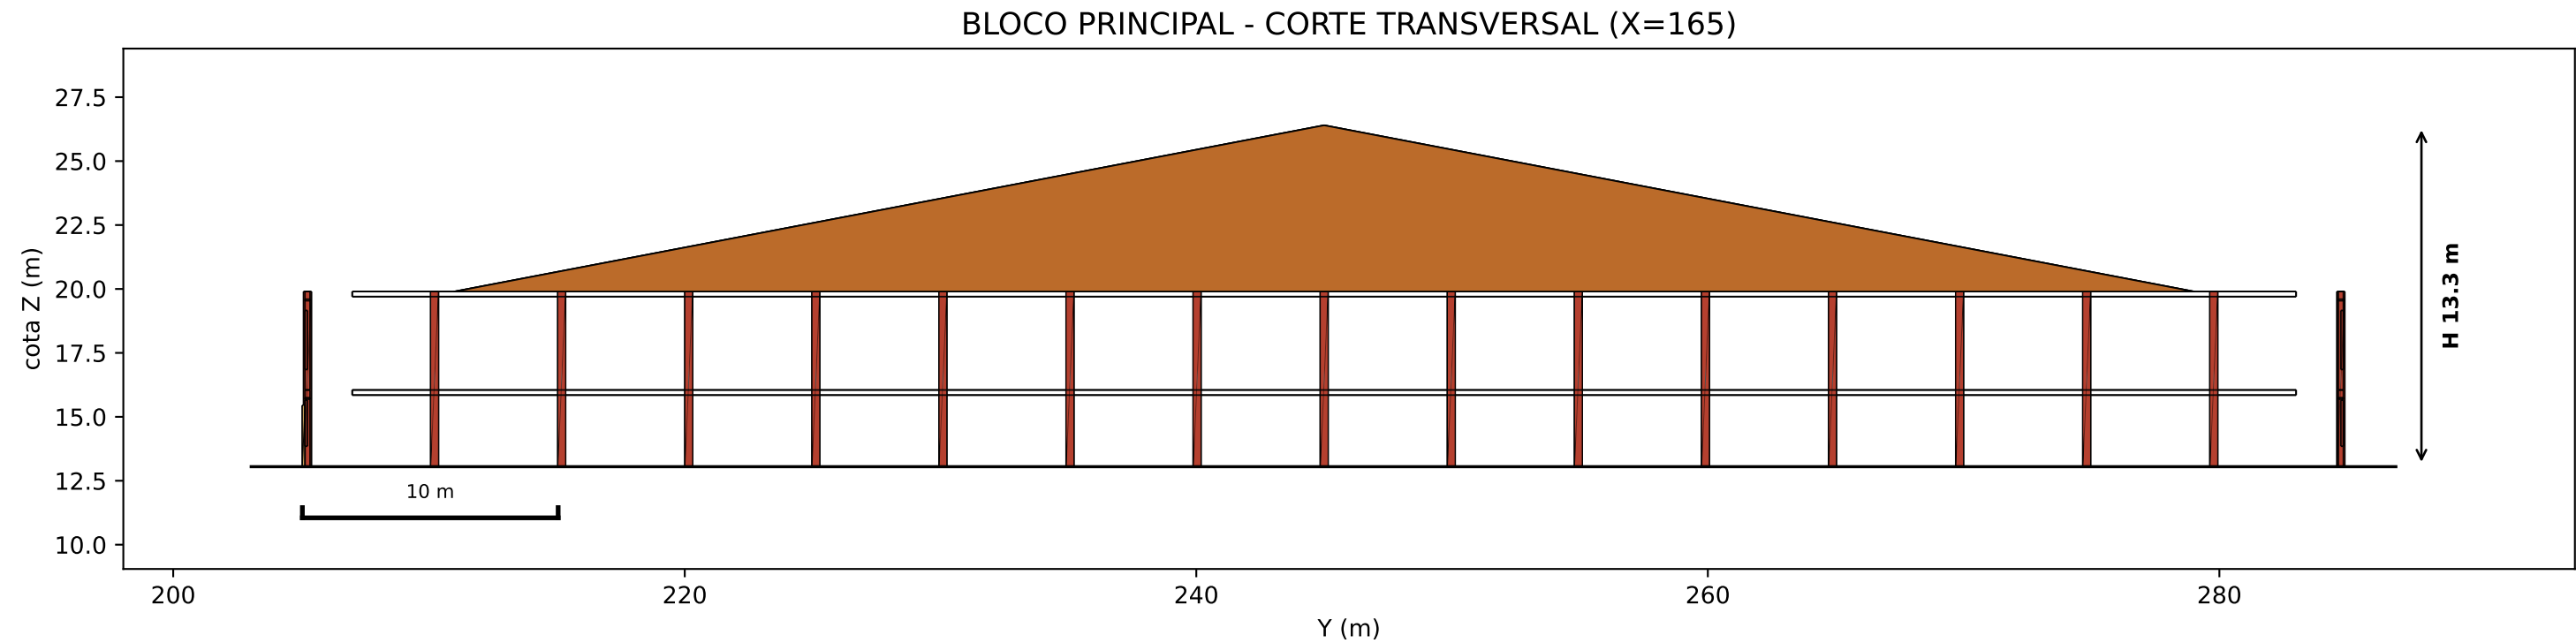

BLOCO A - PLANTA TIPO

HVG BRUMADINHO - Bloco-A-01 - PLANTA TIPO (A01-Terreo) cotada
Ambientes, eixos e pilares - medidas em metros

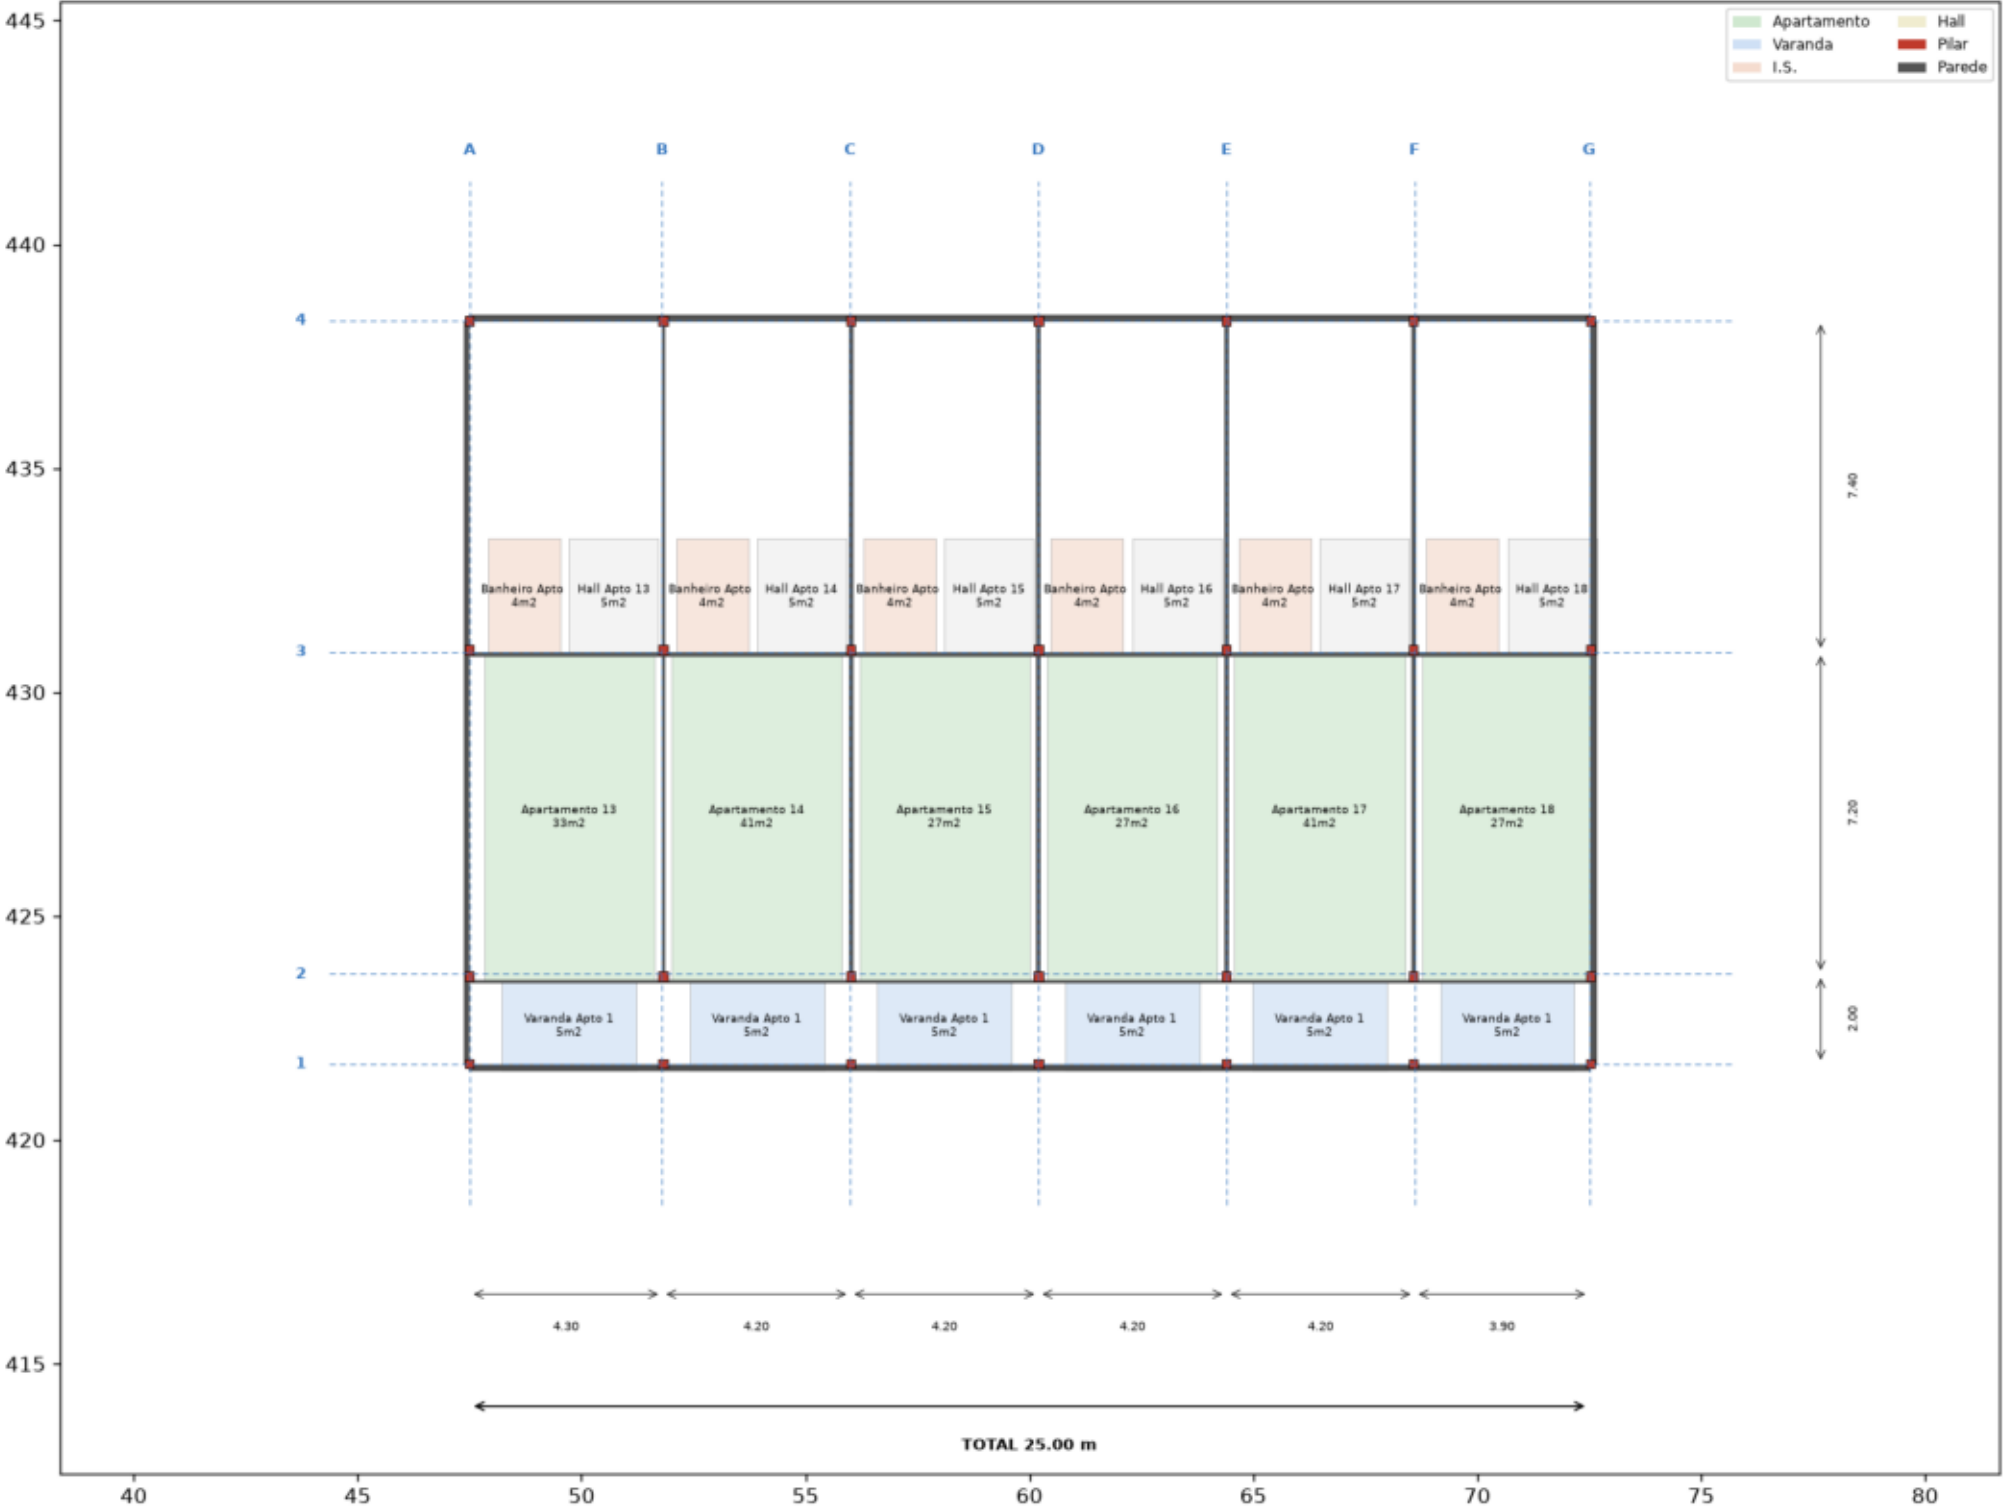

VILA GALE COLLECTION - BRUMADINHO

Country Resort Hotel das Artes, Conference & SPA


PRANCHA

Planta Tipo - Bloco de Apartamentos A

Grupo Montex Ltda - CREA 2101818418
Fase: Licenciamento Data: 06/2026

ESC: barra grafica

BLOCO DE APARTAMENTOS A - FACHADA SUL

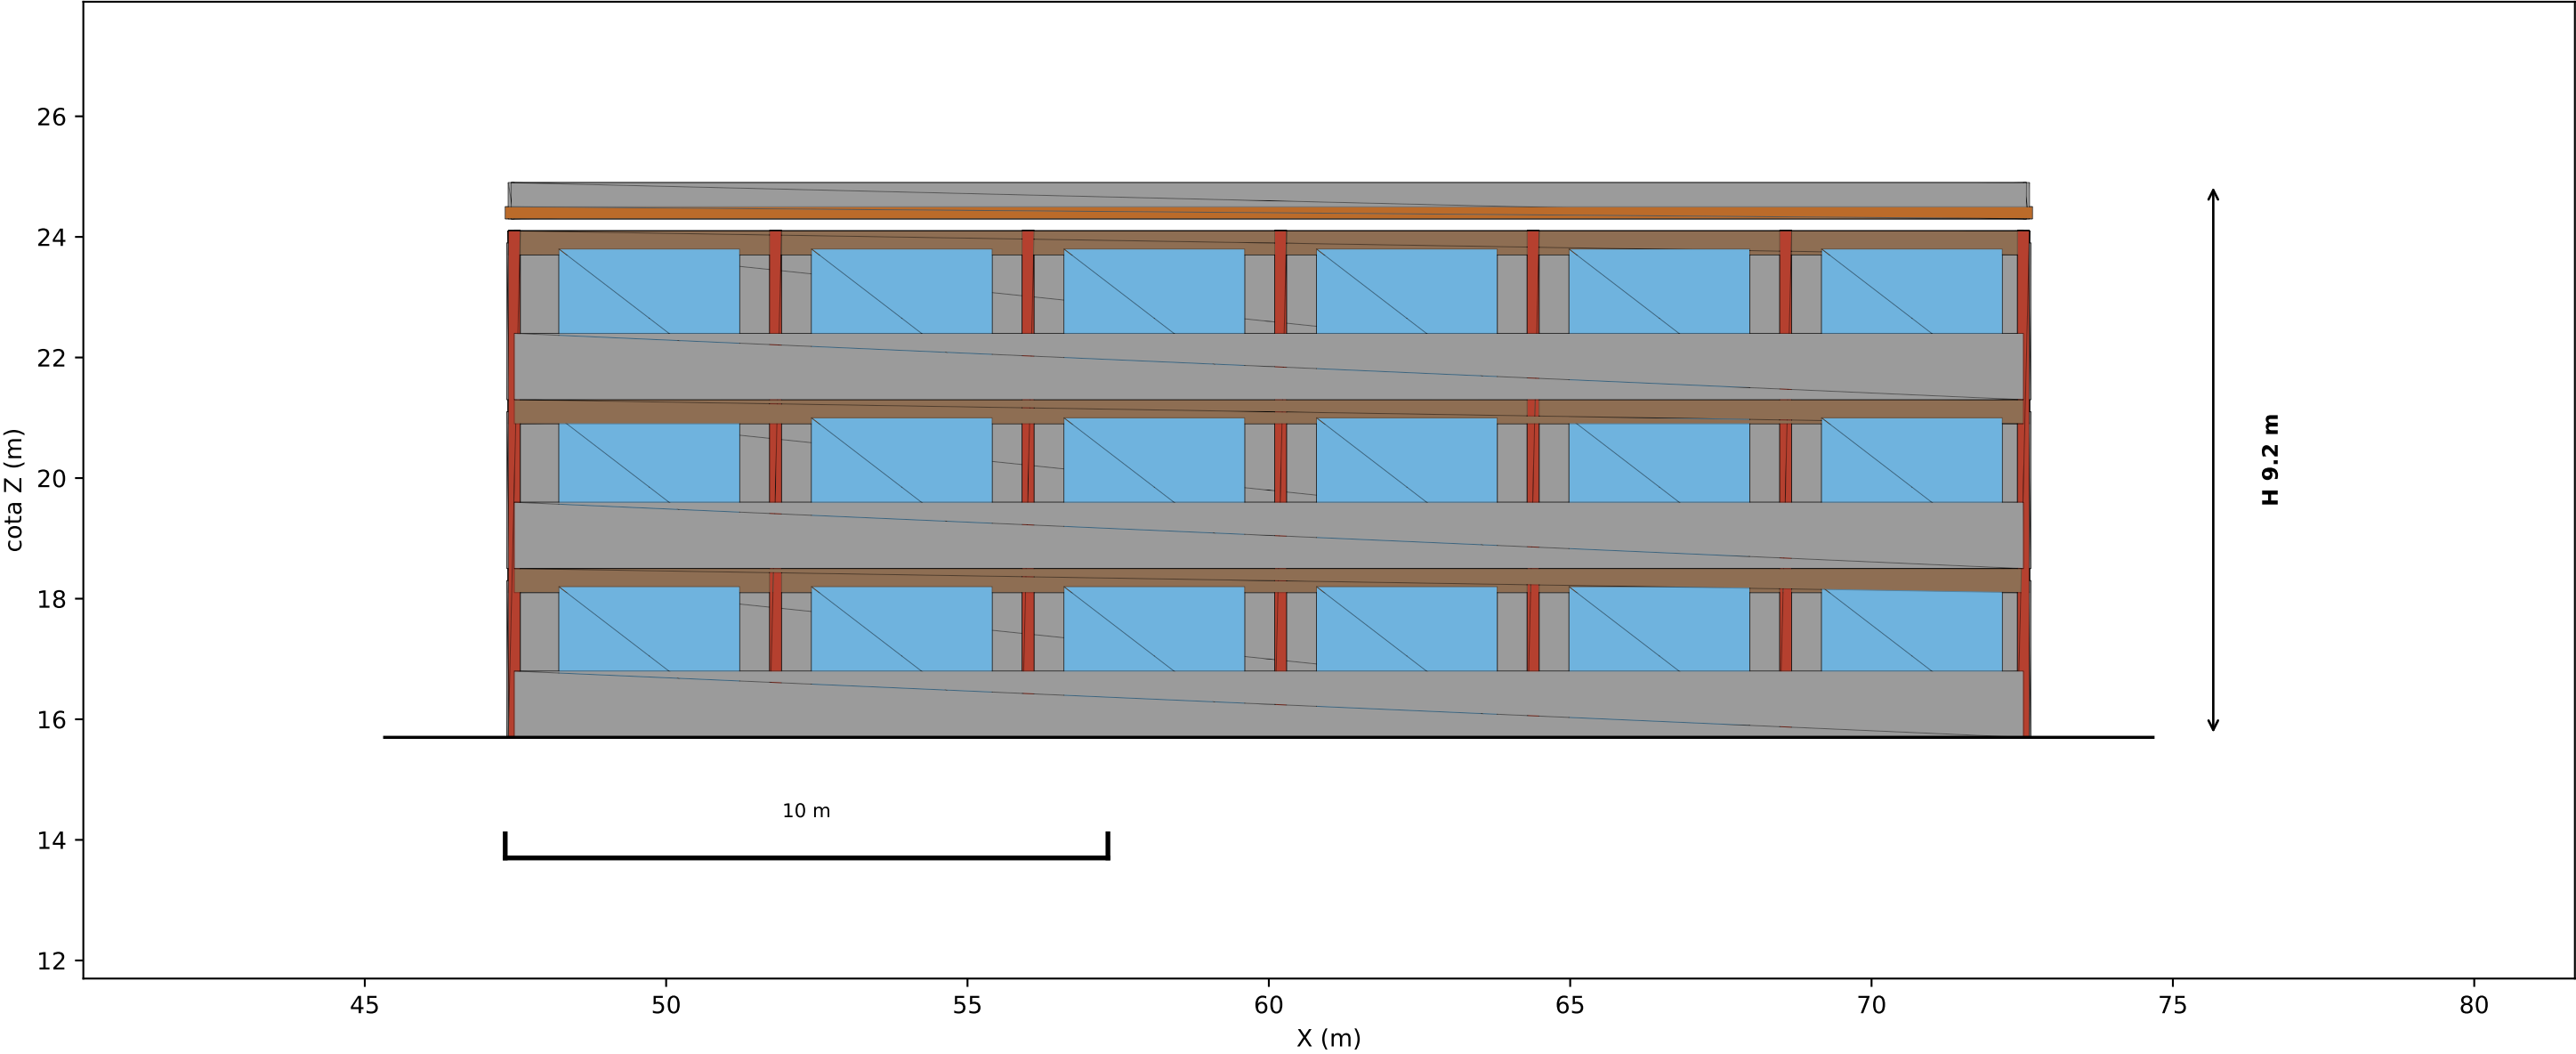

VILA GALE COLLECTION - BRUMADINHO

PRANCHA


Country Resort Hotel das Artes, Conference & SPA

Fachada Sul - Bloco de Apartamentos A

Grupo Montex Ltda - CREA 2101818418
Fase: Licenciamento Data: 06/2026

ESC: barra grafica

BLOCO DE APARTAMENTOS A - CORTE TRANSVERSAL (X=60)

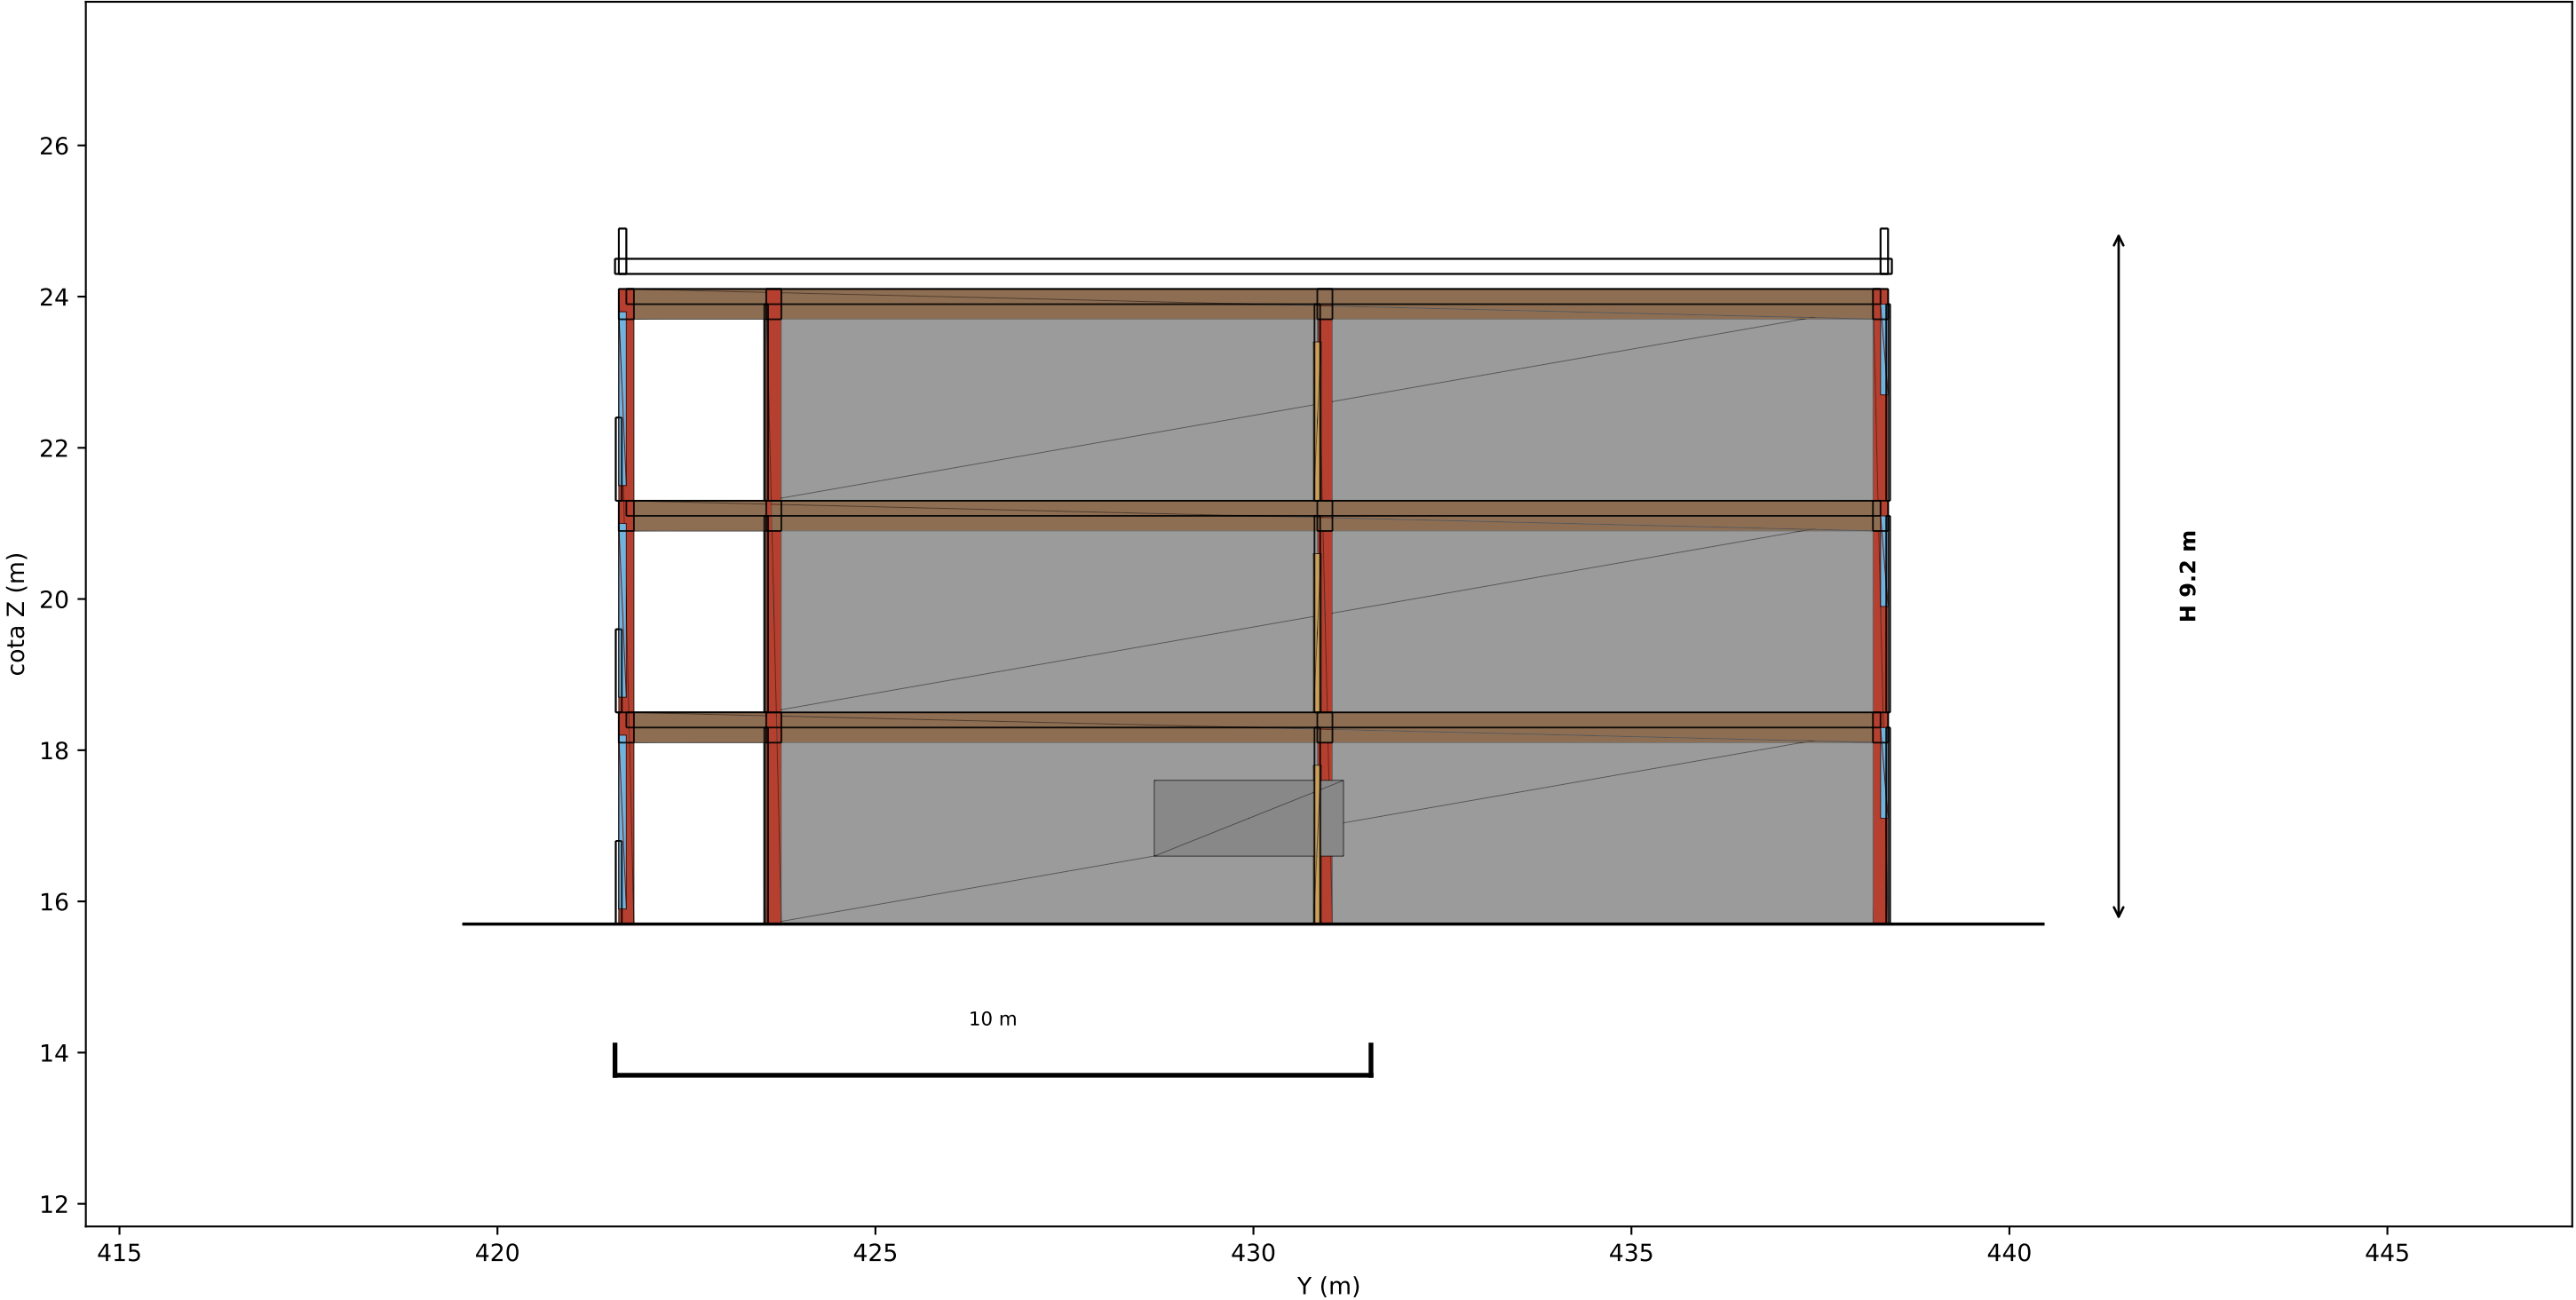

VILA GALE COLLECTION - BRUMADINHO

PRANCHA

Country Resort Hotel das Artes, Conference & SPA


Corte Transversal - Bloco de Apartamentos A

Grupo Montex Ltda - CREA 2101818418
Fase: Licenciamento Data: 06/2026

ESC: barra grafica

BLOCO B - PLANTA TIPO

HVG BRUMADINHO - Bloco-B-13 - PLANTA TIPO (B13-Terreo) cotada
Ambientes, eixos e pilares - medidas em metros

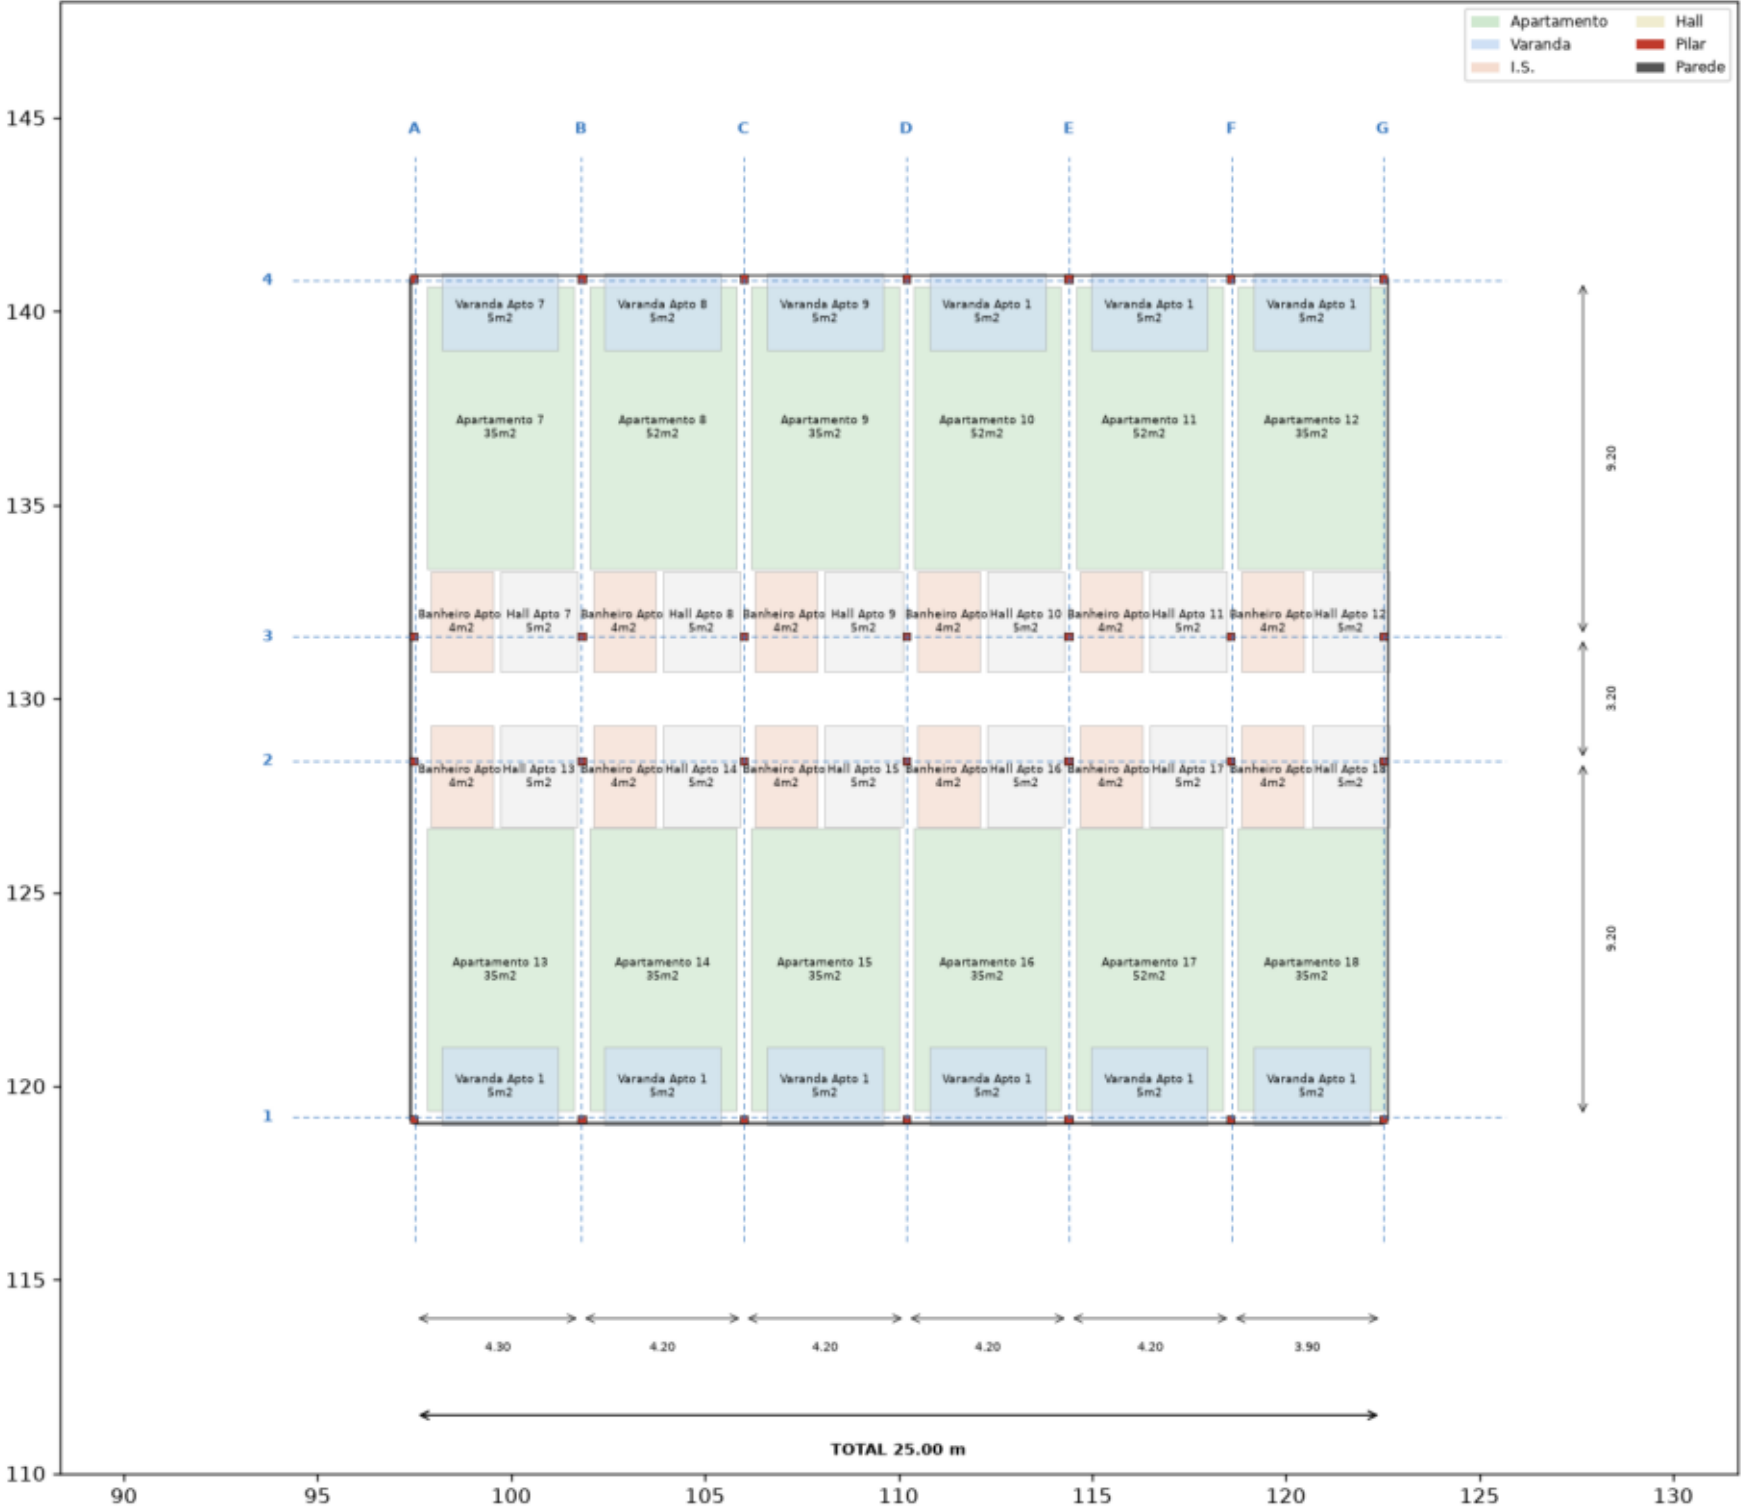

VILA GALE COLLECTION - BRUMADINHO

Country Resort Hotel das Artes, Conference & SPA


Planta Tipo - Bloco de Apartamentos B

Grupo Montex Ltda - CREA 2101818418
Fase: Licenciamento Data: 06/2026

ESC: barra grafica

PRANCHA

BLOCO DE APARTAMENTOS B - FACHADA SUL

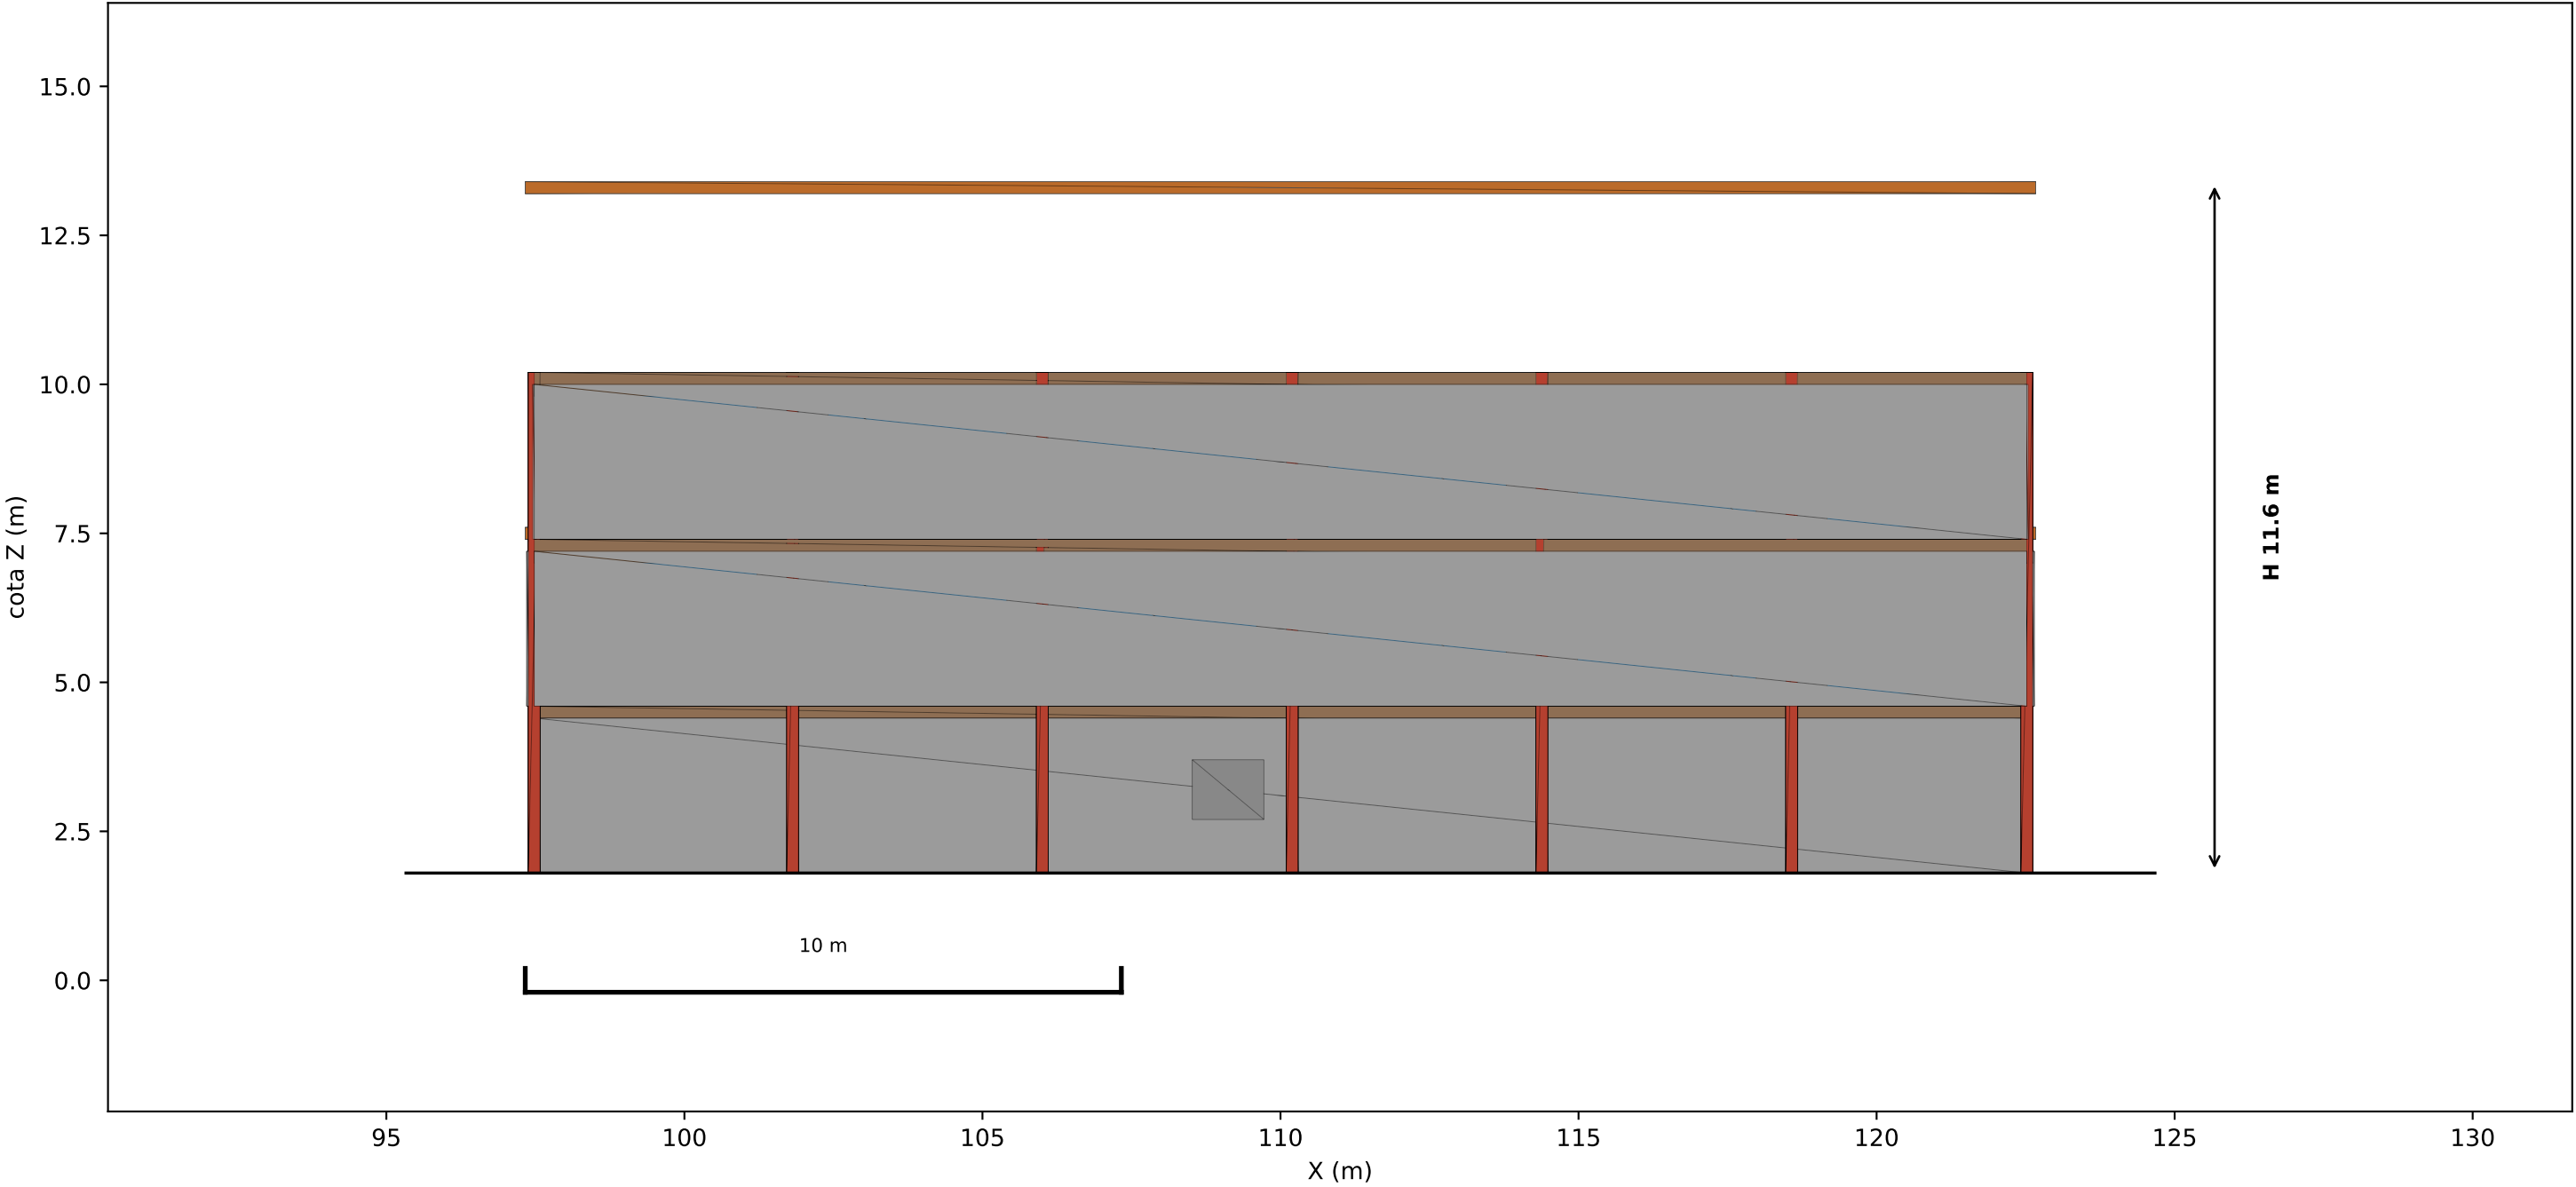

VILA GALE COLLECTION - BRUMADINHO

PRANCHA

Country Resort Hotel das Artes, Conference & SPA

Fachada Sul - Bloco de Apartamentos B

10

Grupo Montex Ltda - CREA 2101818418
Fase: Licenciamento Data: 06/2026

ESC: barra grafica

CRONOGRAMA 4D

HVG BRUMADINHO - CRONOGRAMA 4D (IfcWorkSchedule)
Fases construtivas - elementos vinculados ao IFC

